

YVONNE LI

EDUCATION

Columbia University

Master of Science

Real Estate Development

New York, United States

Aug. 2020 – May 2022

Relevant courses: Real Estate Finance, Fund Management, Private Equity, Real Estate Debt, Global Real Estate Investing, Underwriting, Lease Analysis, Tax Issues in Development, Market Analytics, Real Estate Law, REITs, Capital Markets, Real Estate Entrepreneurialism

Washington University in St. Louis

Bachelor of Science (Double Major)

GPA: 3.4/4.0

Economics, Architecture

St. Louis, United States

Aug. 2016 – Aug. 2019

Relevant courses: *Economics:* Microeconomics, Macroeconomics, Capital Market Imperfections and Entrepreneurial Finance, Labor Economics, Behavioral Economics and Experimental Economics, Econometrics, Statistics, Business Fundamentals

Architecture: Core Design Studios, Sustainable Design, Digital Fabrication, Building System, Drawing

SRISA Florence Summer Program

(Study Abroad)

Florence,

Italy

Topic: Encounters in Public Space (Architecture)

Jul. 2018 – Aug. 2018

EXPERIENCE

CBRE

Financial Intern, FP&A

Los Angeles, United States

Jun. 2022 – Aug. 2022

Recruiting & Retention Project

- Integrated 3 recruiting frameworks into one unified model, achieving a 20% boost in efficiency and standardizing salary structures

Cooperate Finance

- Worked as a team in the elaboration of a 7+5 forecast and benefit realization model, leveraging dashboard and Power BI analytics

- Presented benefit report to upper management with recommendations for maximizing efficiency, based on visualizing 9 key data sets

Group Project

- Won the Capital Allocation by presenting a \$1B M&A proposal incorporating economics analysis, valuations, and projected pro-forma

Cushman & Wakefield

Chengdu, China

Real Estate Strategic Consulting Intern

Feb. 2021 – Jul. 2021

Chengdu Wenjiang District Commercial Real Estate Project

- Strategized commercial development of a 7.5 acre lot as part of a three person team that generated over \$70,000 revenue

- Performed in-depth submarket research, collected government policies and visualized market data into a 118-page final presentation

Chengdu Jinjiang District Cultural Tourism Project

- Performed 18 residential subdistrict interviews, 5 on-site investigations, and 30 phone surveys focus on the submarket

- Visualized historical land prices, economic trends in tourism, and compiled tourism comp sets for analysis report and presentation

Other Project Supports

- Participated in 5 additional real estate projects, a total of 40 telephone interviews, 2 government-related meetings and 1 bidding project, and writing research reports, making PPTs and taking meeting minutes for regulatory meetings as a contributing team member

SPS Dolls

Multiple Cities, China

Founder

Oct. 2019 – Jul. 2021

Stakeholders relations

- Pioneered market-driven product initiatives, secured \$55k in revenue during pandemic challenges, nurtured collaborations with 5 key factories, and capitalized on KOL partnerships for targeted promotions, ensuring a steady cash flow and superior market resonance

Omnichannel retail

- Established stores in two provincial cities, leading a 4-person team from inception to full operation; participated in 4 national doll events, designed 15 doll models, and garnered 3,000+ followers across Instagram, Etsy, and Weibo

SKILLS & CERTIFICATIONS

Professional Skills:

- Advanced Power BI & Data Visualization
- Microsoft Office & Financial Modeling Expertise
- Adobe Creative Suite Proficiency
- AI-Assisted Automation & Analysis
- Strategic Business Planning & Development

Certifications:

- Argus Enterprise
- CFA Level I

Professional Summary

我是一名拥有跨学科经验的 IP 与产品策略制定者。

我的核心能力并不局限于建筑和潮玩设计，而是在复杂环境中识别问题本质，并在审美、结构与市场之间建立长期可持续的连接。

我的创作根源来自小众 BJD 文化与原创 IP 体系，同时拥有商业分析、法律结构与供应链实践经验。擅长在模糊与高压阶段推进方向，能够承担 ownership，并在扁平化团队中高效协作与快速迭代。

Creative & IP Experience

SPS Dolls | IP Founder & Lead Designer

2019 – 2021

SPS Dolls 为 BJD 青年成人向品牌，强调角色气质与人格深度，而非单纯造型风格。

- 构建完整 IP 体系，包括角色背景、审美定位与行为逻辑
- 设计 15+ 款实体产品，涵盖玩偶、陶瓷、树脂、玻璃眼、配件及延展系列
- 负责 4 人小团队管理，从创意开发到发售
- 以小众商品引发对个性的认同感，年营收约 350k

萌萌班 | BJD 品牌（儿童向定位）

萌萌班为更具童感与陪伴属性的品牌方向，与 SPS 的青年气质形成对比，捕捉各个细分兴趣领域的玩家。

Doll Furniture & Accessory Development

我曾开发“蔷薇之匣”等 Doll Furniture 系列，以及玻璃眼等周边产品。擅长发现市场空白，仅凭甚美和需求产出多个高溢价（售价约成本 12.5 倍）的产品。

Plush Toy Market Exploration (Dongguan & Yangzhou)

东莞与扬州的毛绒玩具供应链探索，是一次未完全实现的尝试，但对我意义重大。

让我可以深度调研毛绒材料与制造工艺，深入工厂生产线体验。评估成本结构与打样流程并理解“可生产性”对 IP 设计的限制。

Brand & Lifestyle Strategy

Brand Development (Project-based) | US Furniture Brand | 2024

品牌叙事：负责 Ins 运营与品牌转型的视觉逻辑，把控品牌调性，将品牌从原始的“功能性物件”重塑为“生活审美载体”。吸引有审美的粉丝和引起对于品质生活的想象和共鸣。

博主共创：策划并执行与高质感 Influencers 的视频联动，通过艺术化叙事提升品牌在北美市场的溢价能力。

Business & Structural Experience

New Dream Services | Legal Document Assistant (California Registered LDA)

- 处理复杂法律文书与商业结构问题
 - 参与移民、创业与企业合规结构分析
-

Cushman & Wakefield | Consultant

CBRE | Financial Intern

- 商业地产项目可行性分析，市场调研与财务模型构建，资产与投资逻辑理解。多元化经济和金融背景可以更好的理解和推动 IP 的商业化。
-

AI Companion Design Perspective

2024年在日本线下接触 Lovot 之后，我开始思考 AI 陪伴产品的结构问题。

我认为，当前中国 AI 玩偶的核心问题不在技术，而在：过度强调功能与对话，大多数 AI 毛绒/IP 都是一个 AI 聊天盒子加一个毛绒外表。同质化严重。缺乏 IP 连续性，无法让用户有持续兴趣和购买冲动且无法达到情绪价值带来的的高溢价。

未来 AI IP 发展更倾向于减少“机器感”，产品 IP 化，更有人感，且将技术隐形化

Problem Solving & Ownership

- 越复杂的问题越能体现我的价值。在 IP 形象设计中，我本人在艺术，哲学，运动和学习中接触的多面性思考和通才的特性可以帮助 Solulu 产出更立体的 IP 形象。也希望团队可以更了解我本人之后再去下定义我和岗位的适配性。
- 擅长拆解本质而非处理表象。大多产品都是从 0 开始的实践，更适合团队初创现状。
- 抗压能力强，适应高节奏环境，但不急于追求结果，而是更看重思考与过程。
- 接受反馈并快速迭代，愿意与 IP 共成长。
- 既能独立推进，也能深度参与团队协作。兴趣驱动价值，可以相信我有无限的创造力和想象力。

Table of Content



Bath House |
Green House




the
Playground




Theater
with Two
Characters



4101
Laclede

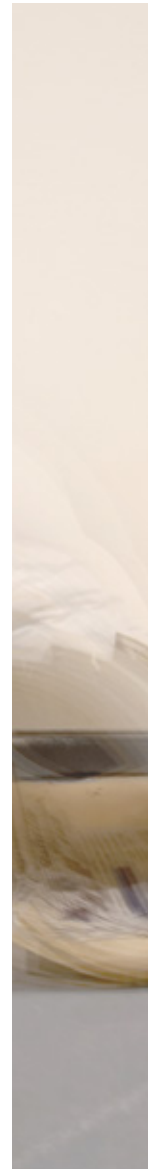

Snail
Rocker

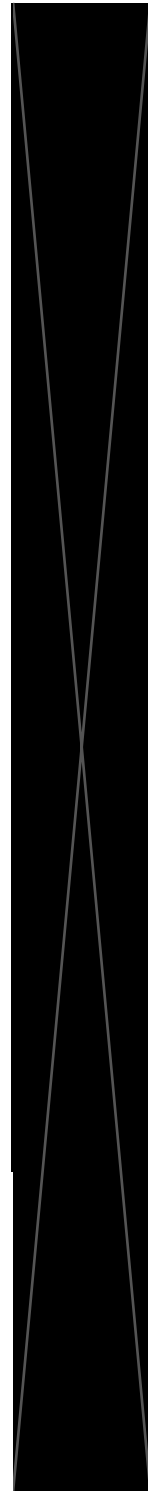


Echeveria elegans
(Mexican Snowball)



Adult Echeveria and
Propagation Stages,
Graphit and Watercolor.

Echeveria Cells
under Microscope
Watercolor
36*24in

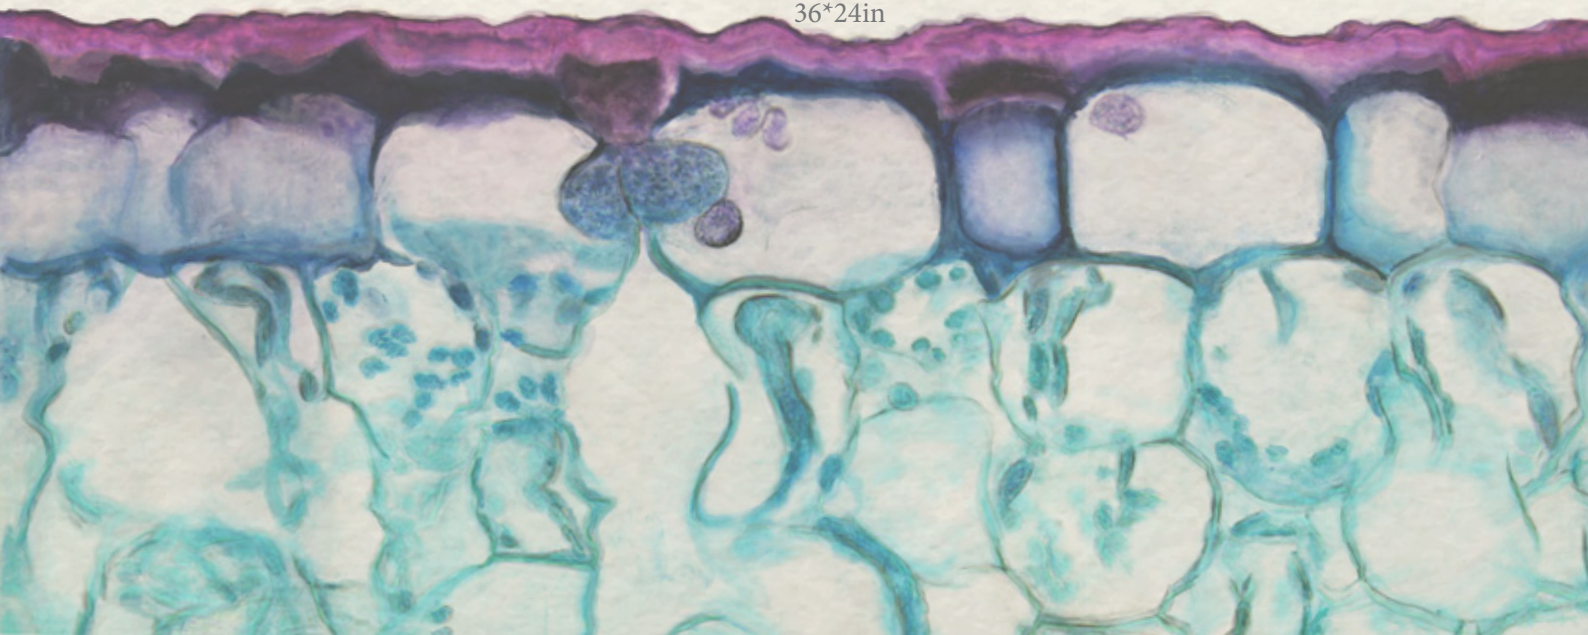

Greenhouse | Bathhouse

Studio 212 | 2018 Spring
Jesse Vogler

This project focuses on the thermal and programmatic adjacencies within the building, as well as the urban and social relationships with a specific site. Starting from analytical researches on selected plants, I designed the Eco-Unit based on the botanical features and environment, and then design the bathhouse and greenhouse with a deeper investigation in Eco-Unit.

Eco Unit



The opening on the top
allows plant to grow freely
without any obstruction

The structural skin system not
only provides support to the
plant but also leave growing
space for the baby plants

Pot with cone-shaped facilities

Before designing the actual Greenhouse, We started out with Eco Unit for single plant. According to the survival requirements of my plant, I customized a Eco Unit for her, which could sustain itself without further attention.

My Echeveria survived for the whole semester and even grew taller than it was planted in the Eco Unit.



Eco Unit



Pot and Echeveria



The cone-shaped skin structure
plugs in onto the pot without any
other connections necessary.
Cone-shaped skin

The skin could be easily put on and taken off from the flower pot. Since the skin itself is strong enough to provide protection to the plant inside, I would therefore focus on this feature of the structure.

Verb List | sunlight and water

glow

glitter

beam

hit

contact

dash

spray

plash

splatter

groove

pipe

transmit

drip

trickle

leak

drop

Illuminate

Shine

Gleam

Touch

Reflect

Splash

Penetrate

Channel

Drain

Dribble

Flood

lighten

elucidate

brighten

enlighten

glare

glint

echo

mirror

reproduce

permeate

puncture

drill

drip

sap

deplete

exhaust

deluge

rush

overflow


Model 6
Flattened Collage




The common verb that both sunlight and water could used to describe is “to penetrate”.

So I did a series of concept models regarding to this verb using different materials and techniques.

Instead of building the block out of skeletal struc-
ture, I rather take out some material and let the
negative space be the primary structure.

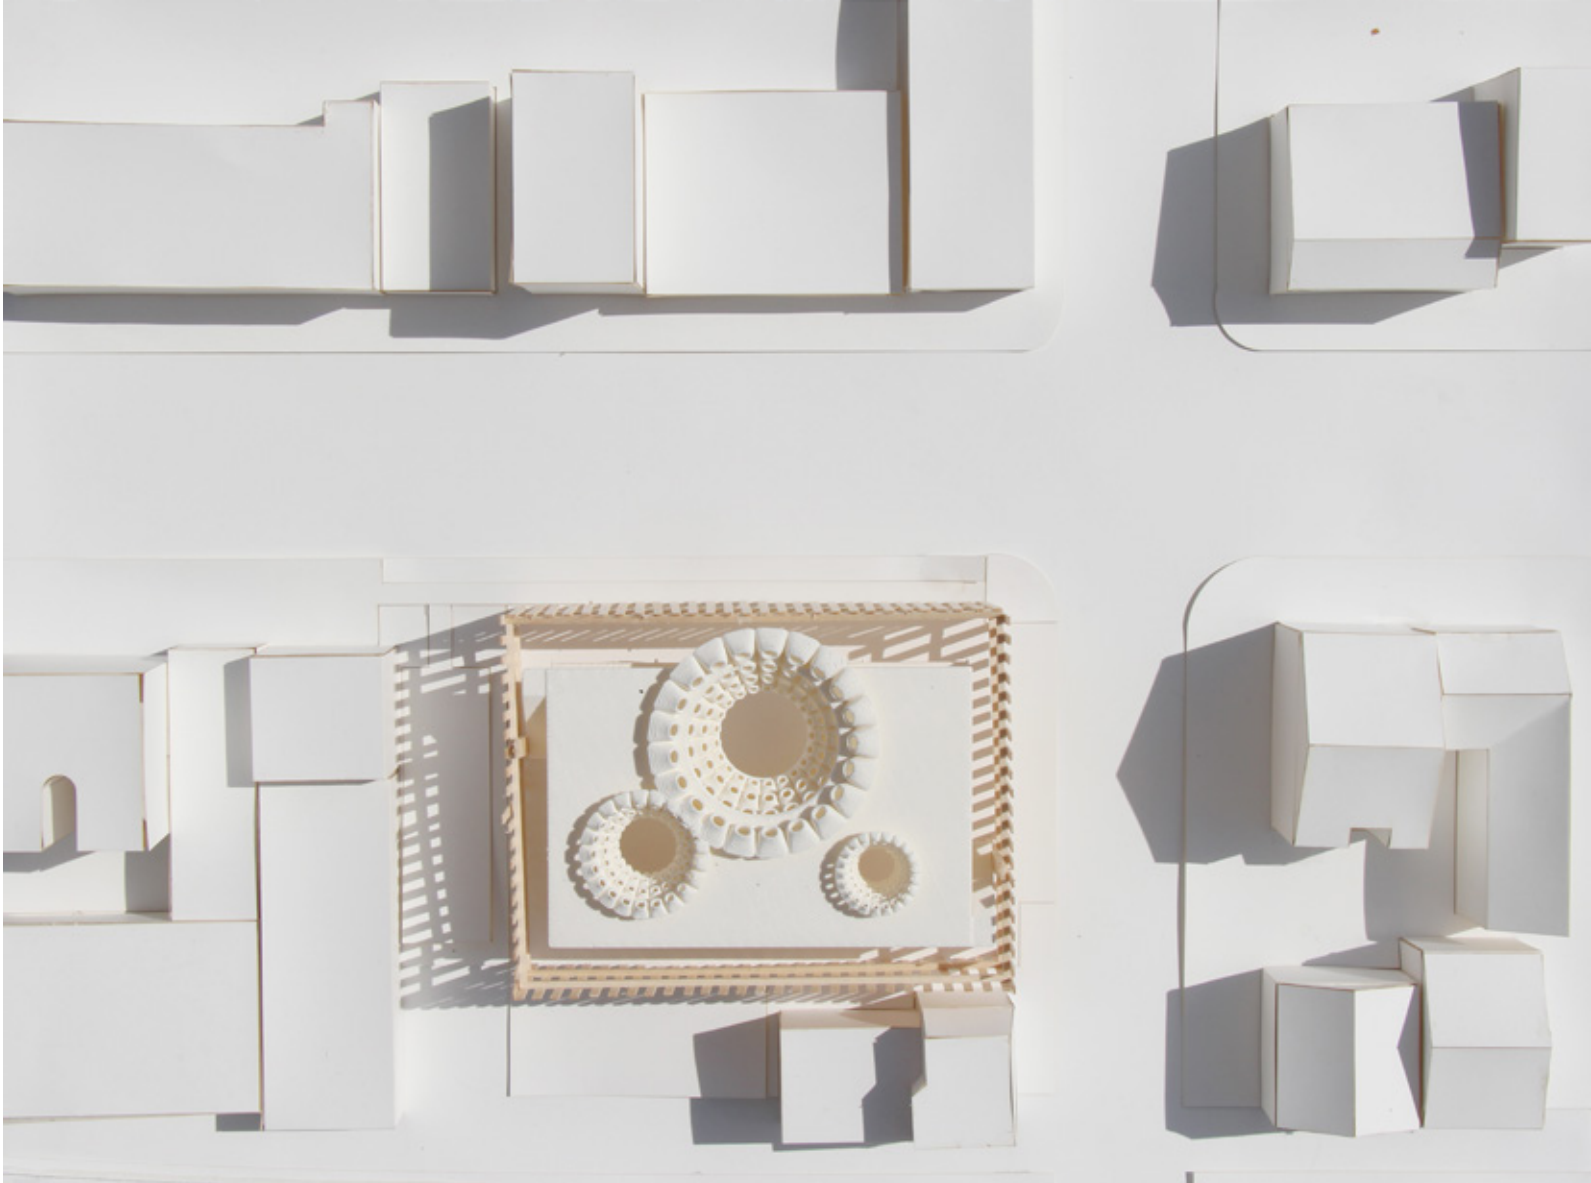

1'=1/16" Scale model with
Site

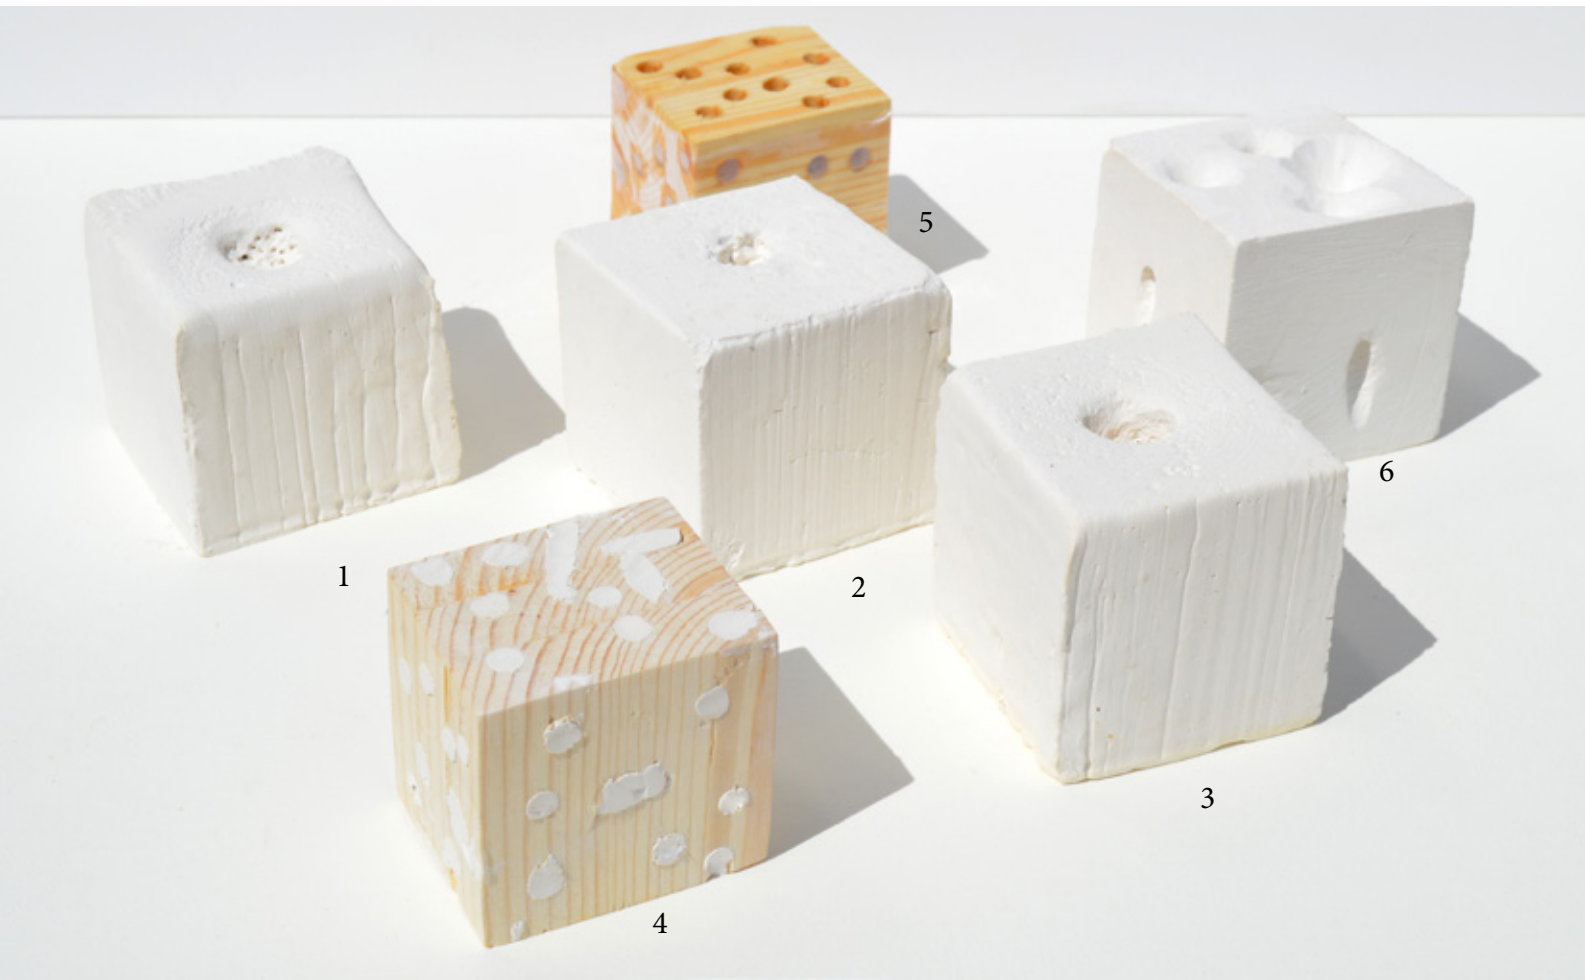

1 | 2 | 3

Three identical plaster cubs placed under dripping water for dif-
ferent length to test out how water could shape other materials.

4 | 5

Wood cubes with hole at different angles, displaying the surface
condition of the negative space.

6 |

Using conclusions drawn for the previous 5 models, this model
shows how different holes at different angles could perform in a
building.

7 |

Negative space created by the same geometry used in the Eco-
Unit





Site


The site is in the historic Soulard neighborhood and is a corner, urban lot. In the process of investigating the site, I found that there are several different types of support system used by different forms of buildings. In the process of figuring out the evolution in support systems of the Domino house and the Sendai Mediatheque, my project primarily focuses on the support solely.



Support Systems on Site
1/32"=1'0"

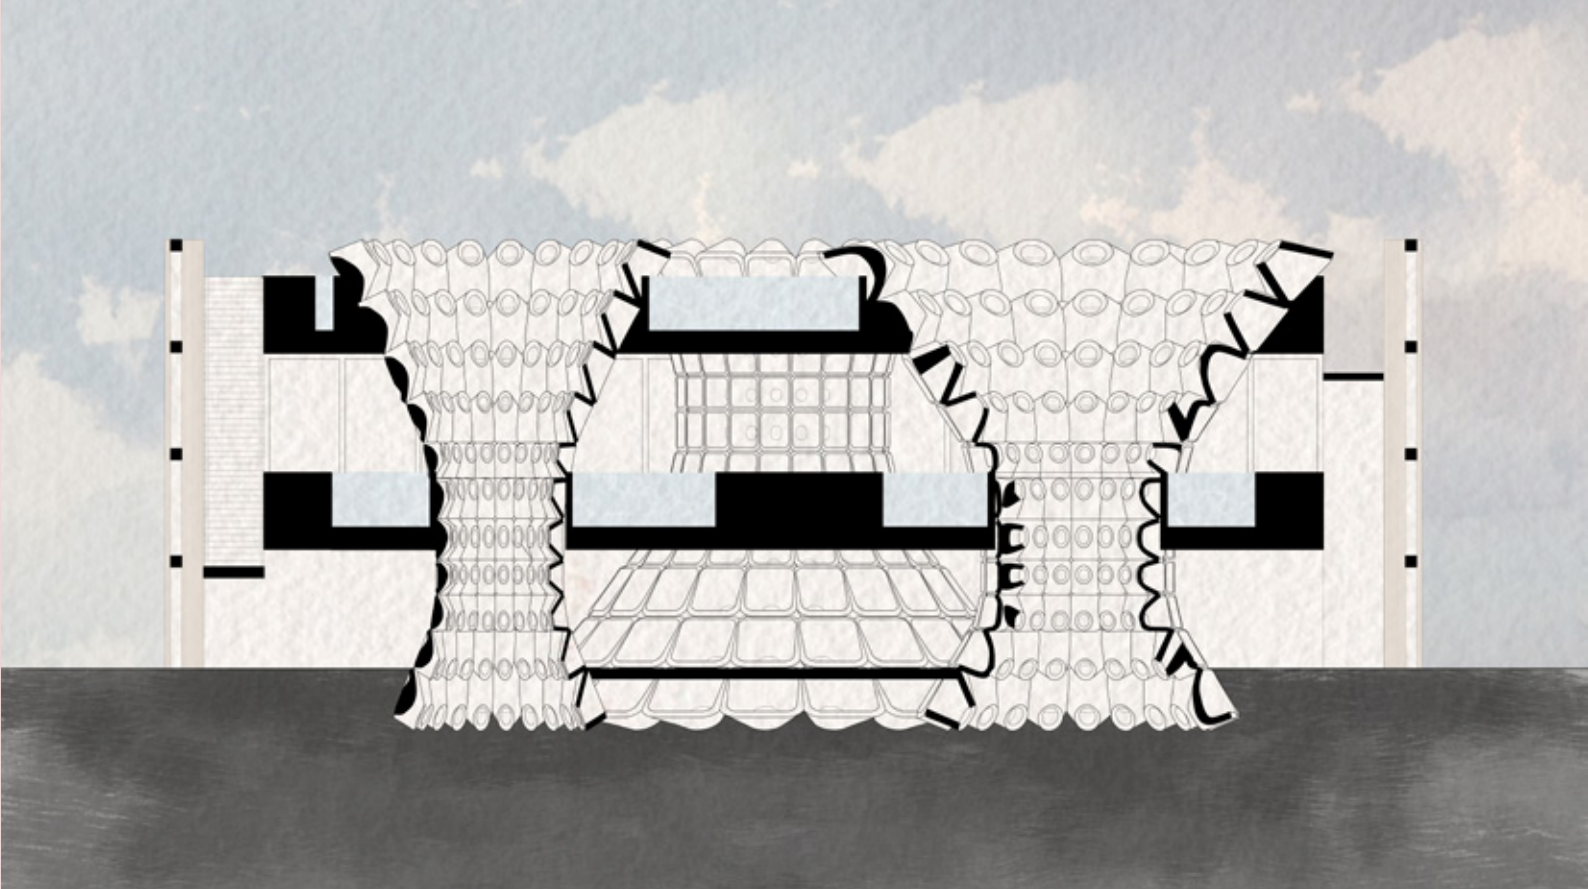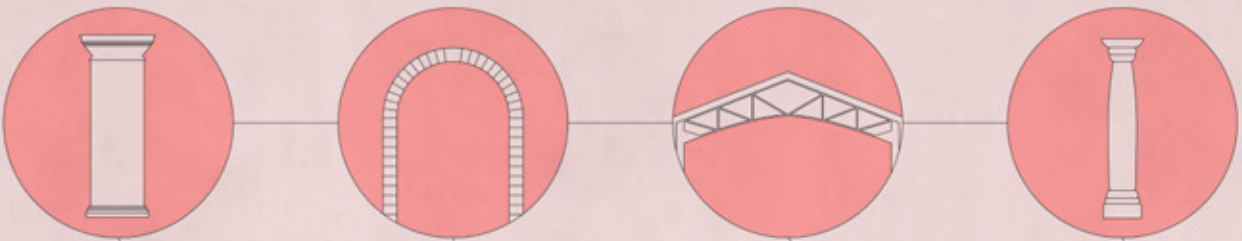

Section Drawing

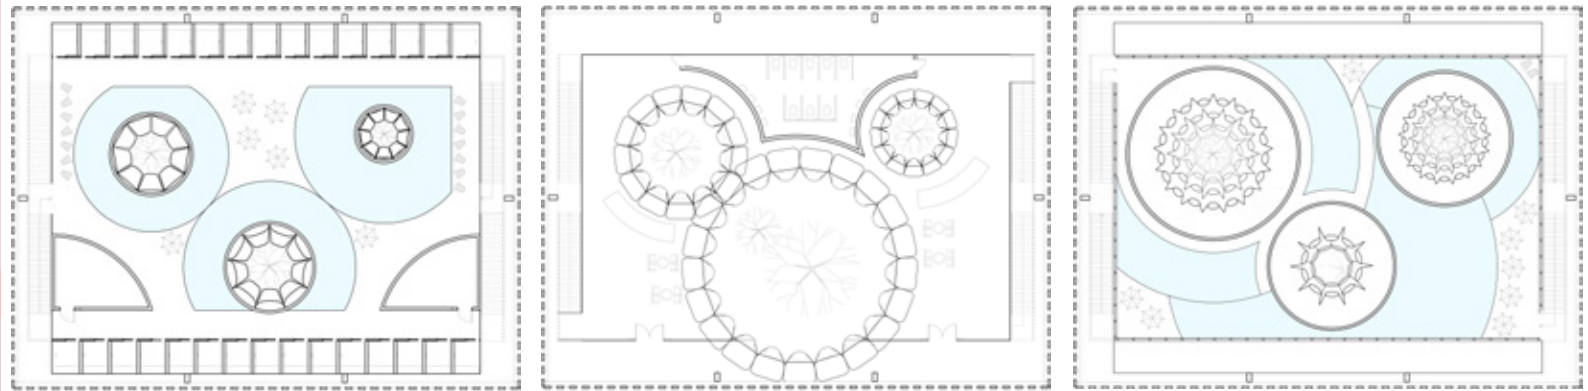

Floor plans



Interior Render



5,710 children who crossed the Mediterranean last year were unaccompanied. A total of 25,846 children made the crossing.



-Victor, 5


Victor was rescued from the Mediterranean Sea after being separated from his mother. Victor was detained in Surman detention center for nearly two months.



-Kamir, 9

"They arrested us and brought us into the Zawia prison. No food. No water. They beat us every day. No doctor, no medicine."



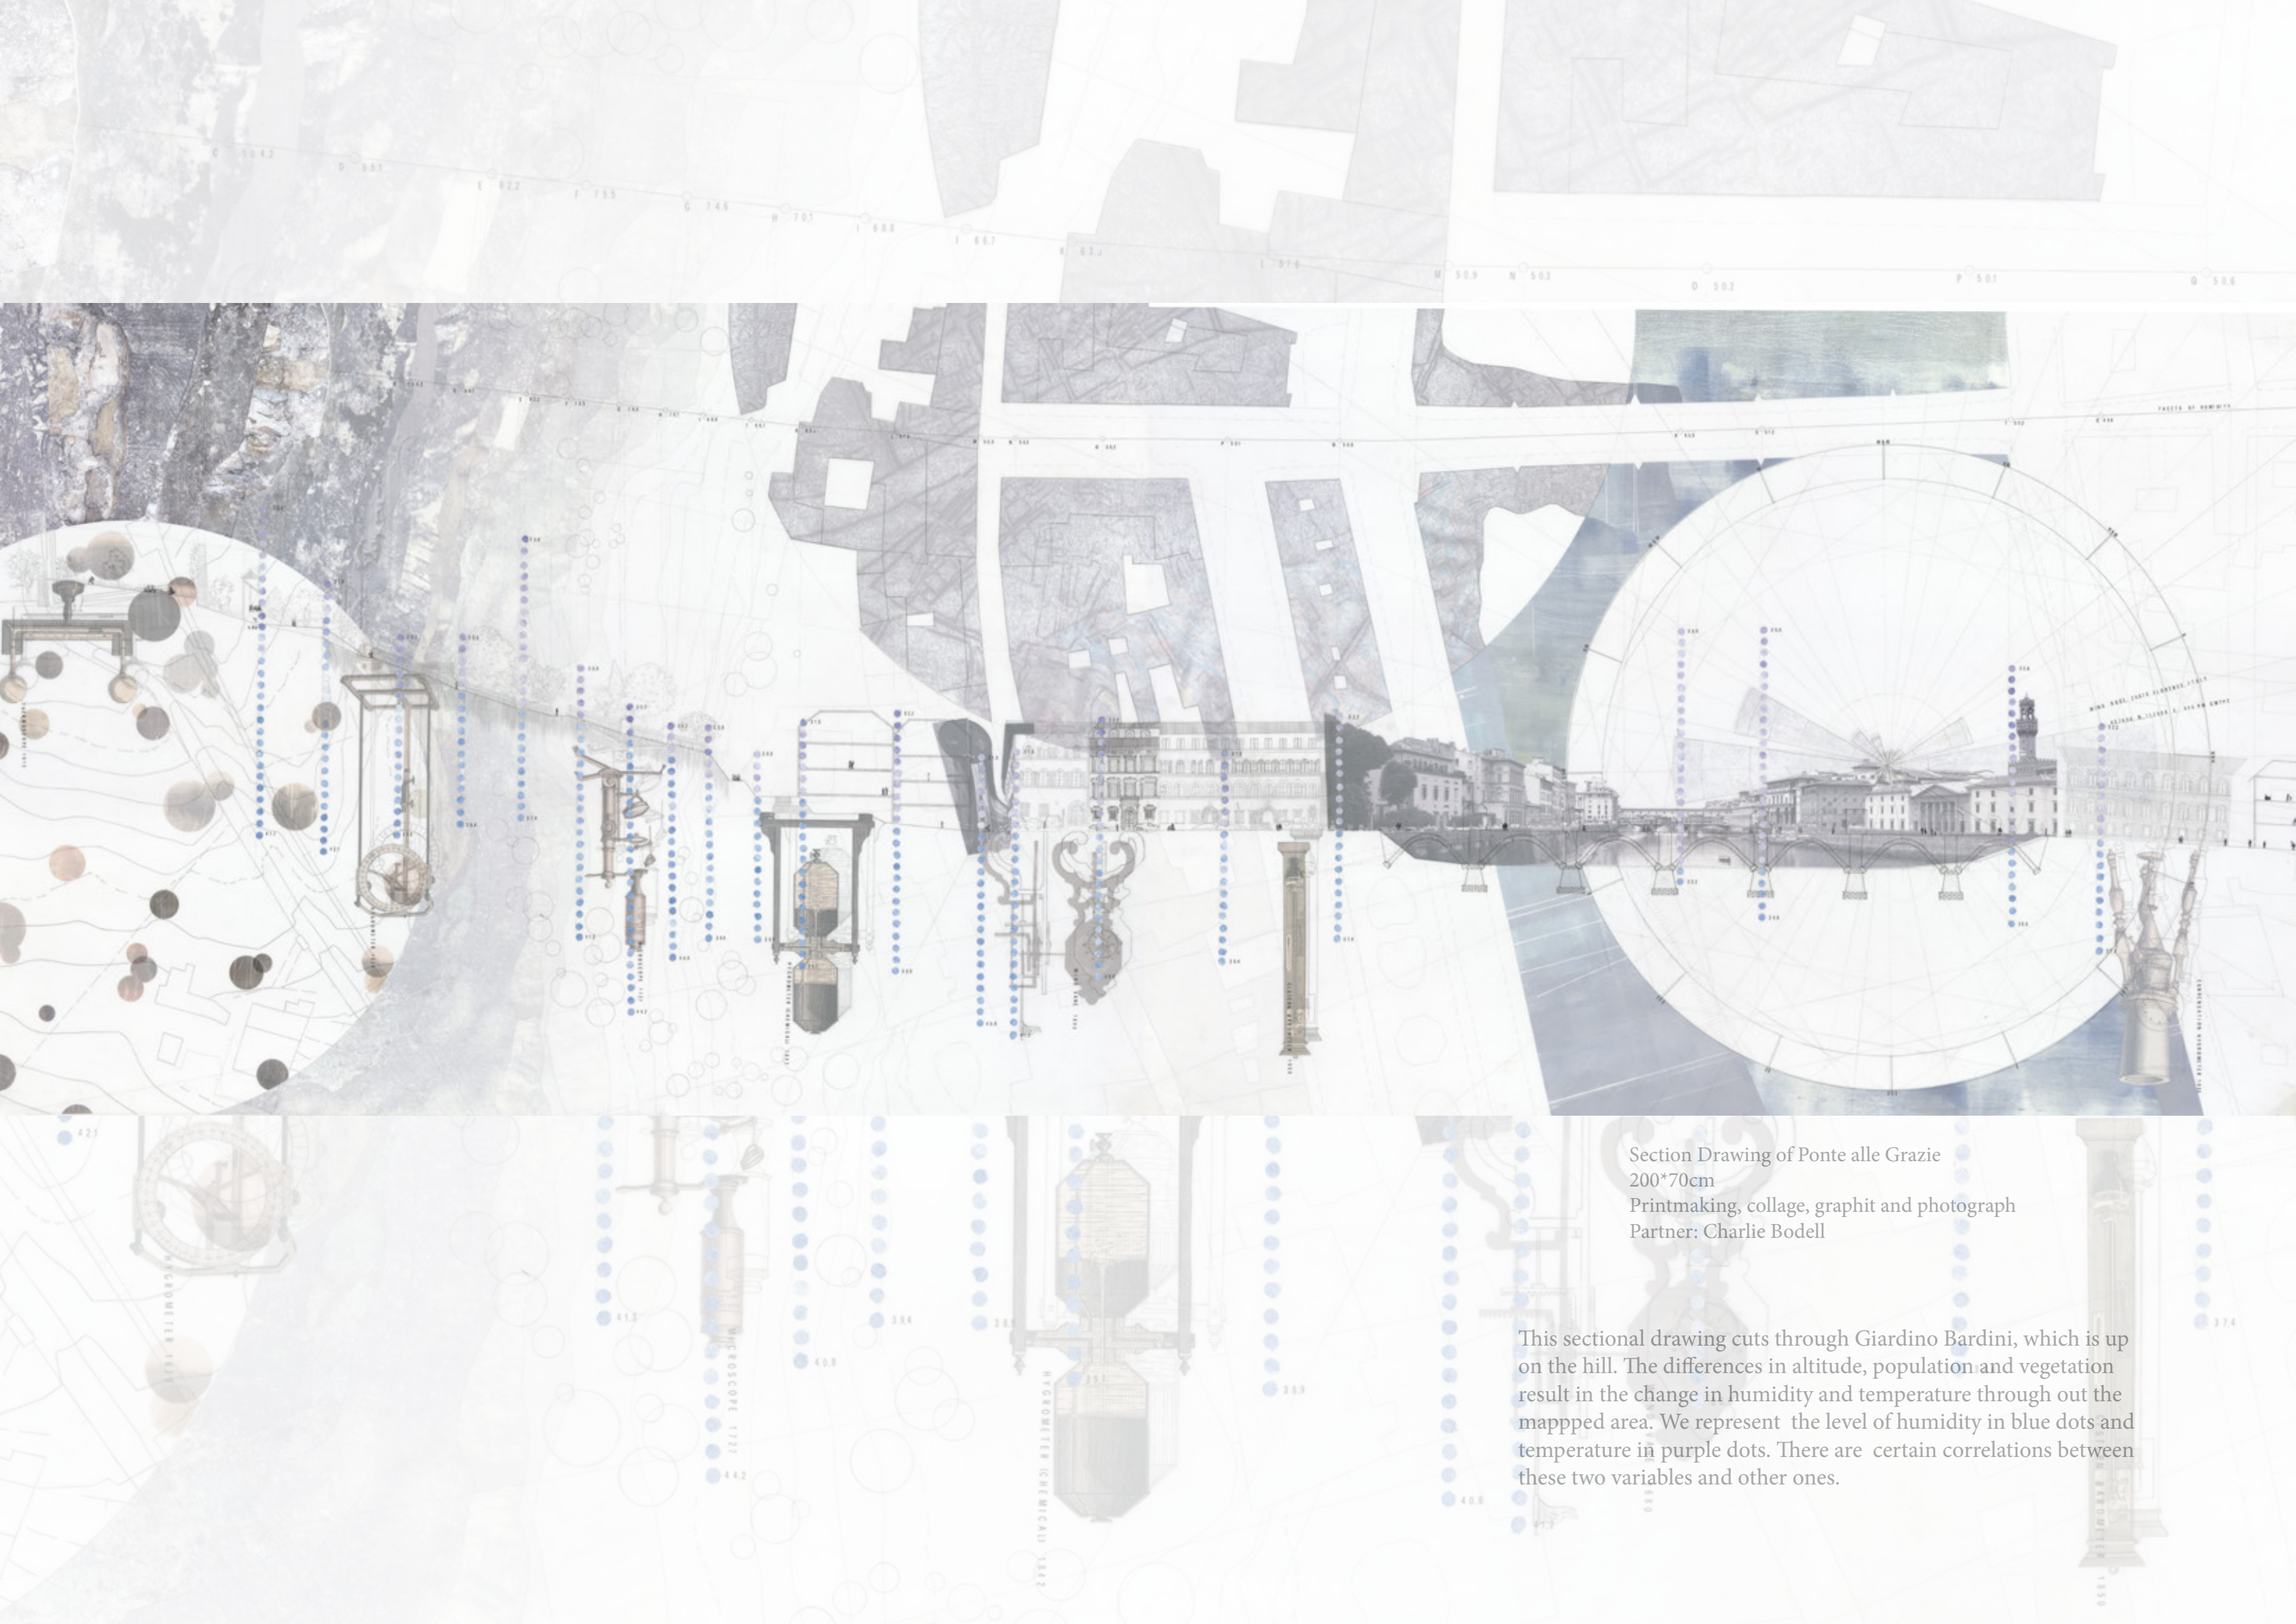

Section Drawing of Ponte alle Grazie
200*70cm
Printmaking, collage, graphit and photograph
Partner: Charlie Bodell

This sectional drawing cuts through Giardino Bardini, which is up on the hill. The differences in altitude, population and vegetation result in the change in humidity and temperature through out the mapped area. We represent the level of humidity in blue dots and temperature in purple dots. There are certain correlations between these two variables and other ones.




Plan

Section

City Wall Montessori Kindergarten
 Inspired by the previous project Humidity Map , I want to build a kindergarten for both young refugees and local children. The shape of this kindergarten follows along the edge of the old Florence city wall. Two classroom doors are facing each other in order to facilitate the connection among children.

Each area of the classrooms are planned by many smaller circles where the whole kindergraten builds on a bigger circlce.

The utilization of circles presents a orbicular image which visions the reunion of refugee families.

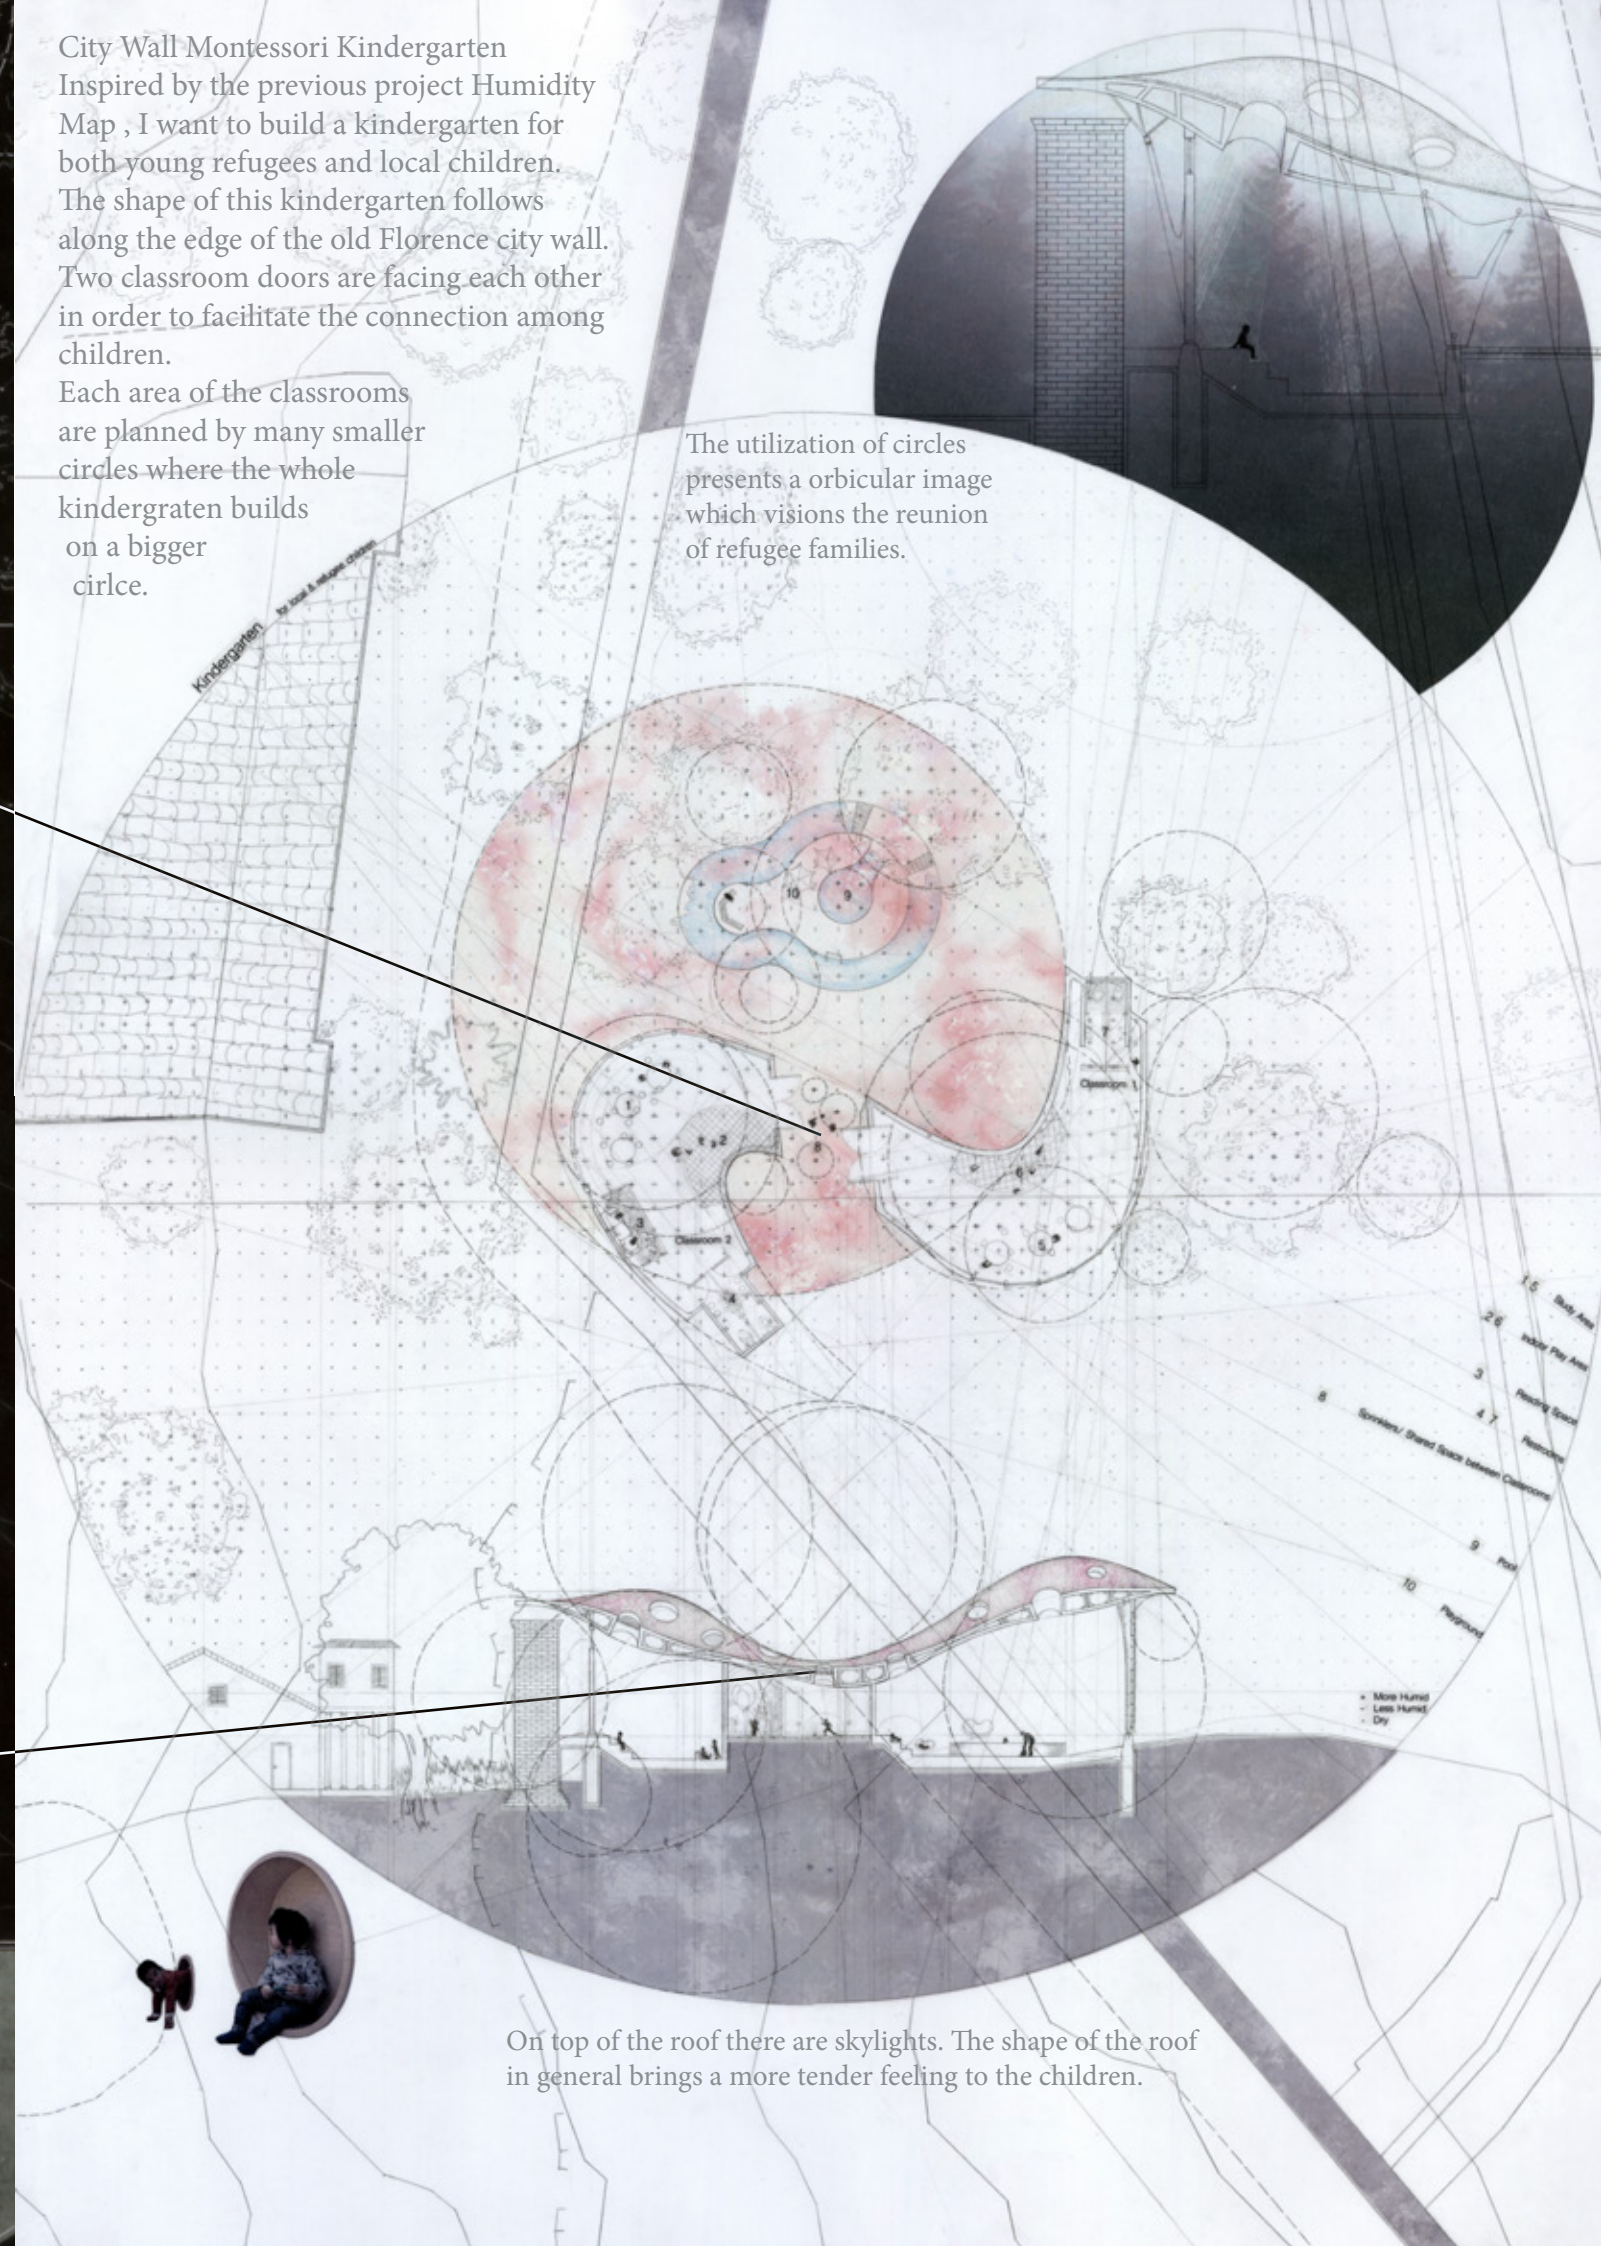

On top of the roof there are skylights. The shape of the roof in general brings a more tender feeling to the children.

Observatory

Studio III | 2016 Fall
Igor Marjanovic

The design from an negative space drawing of the organic pattern, and then it went to the basswood and wire model, and after that, the observatory for the nature.



Natural Pattern
Photograph
Site: St. Louis Forest Park


Basswood Iteration
Basswood Sticks
36*24in

Wire Iteration
Piano Wire
15*20in

Pattern tracing drawing
36*24in Graphit

Observatory
Basswood
20*12in

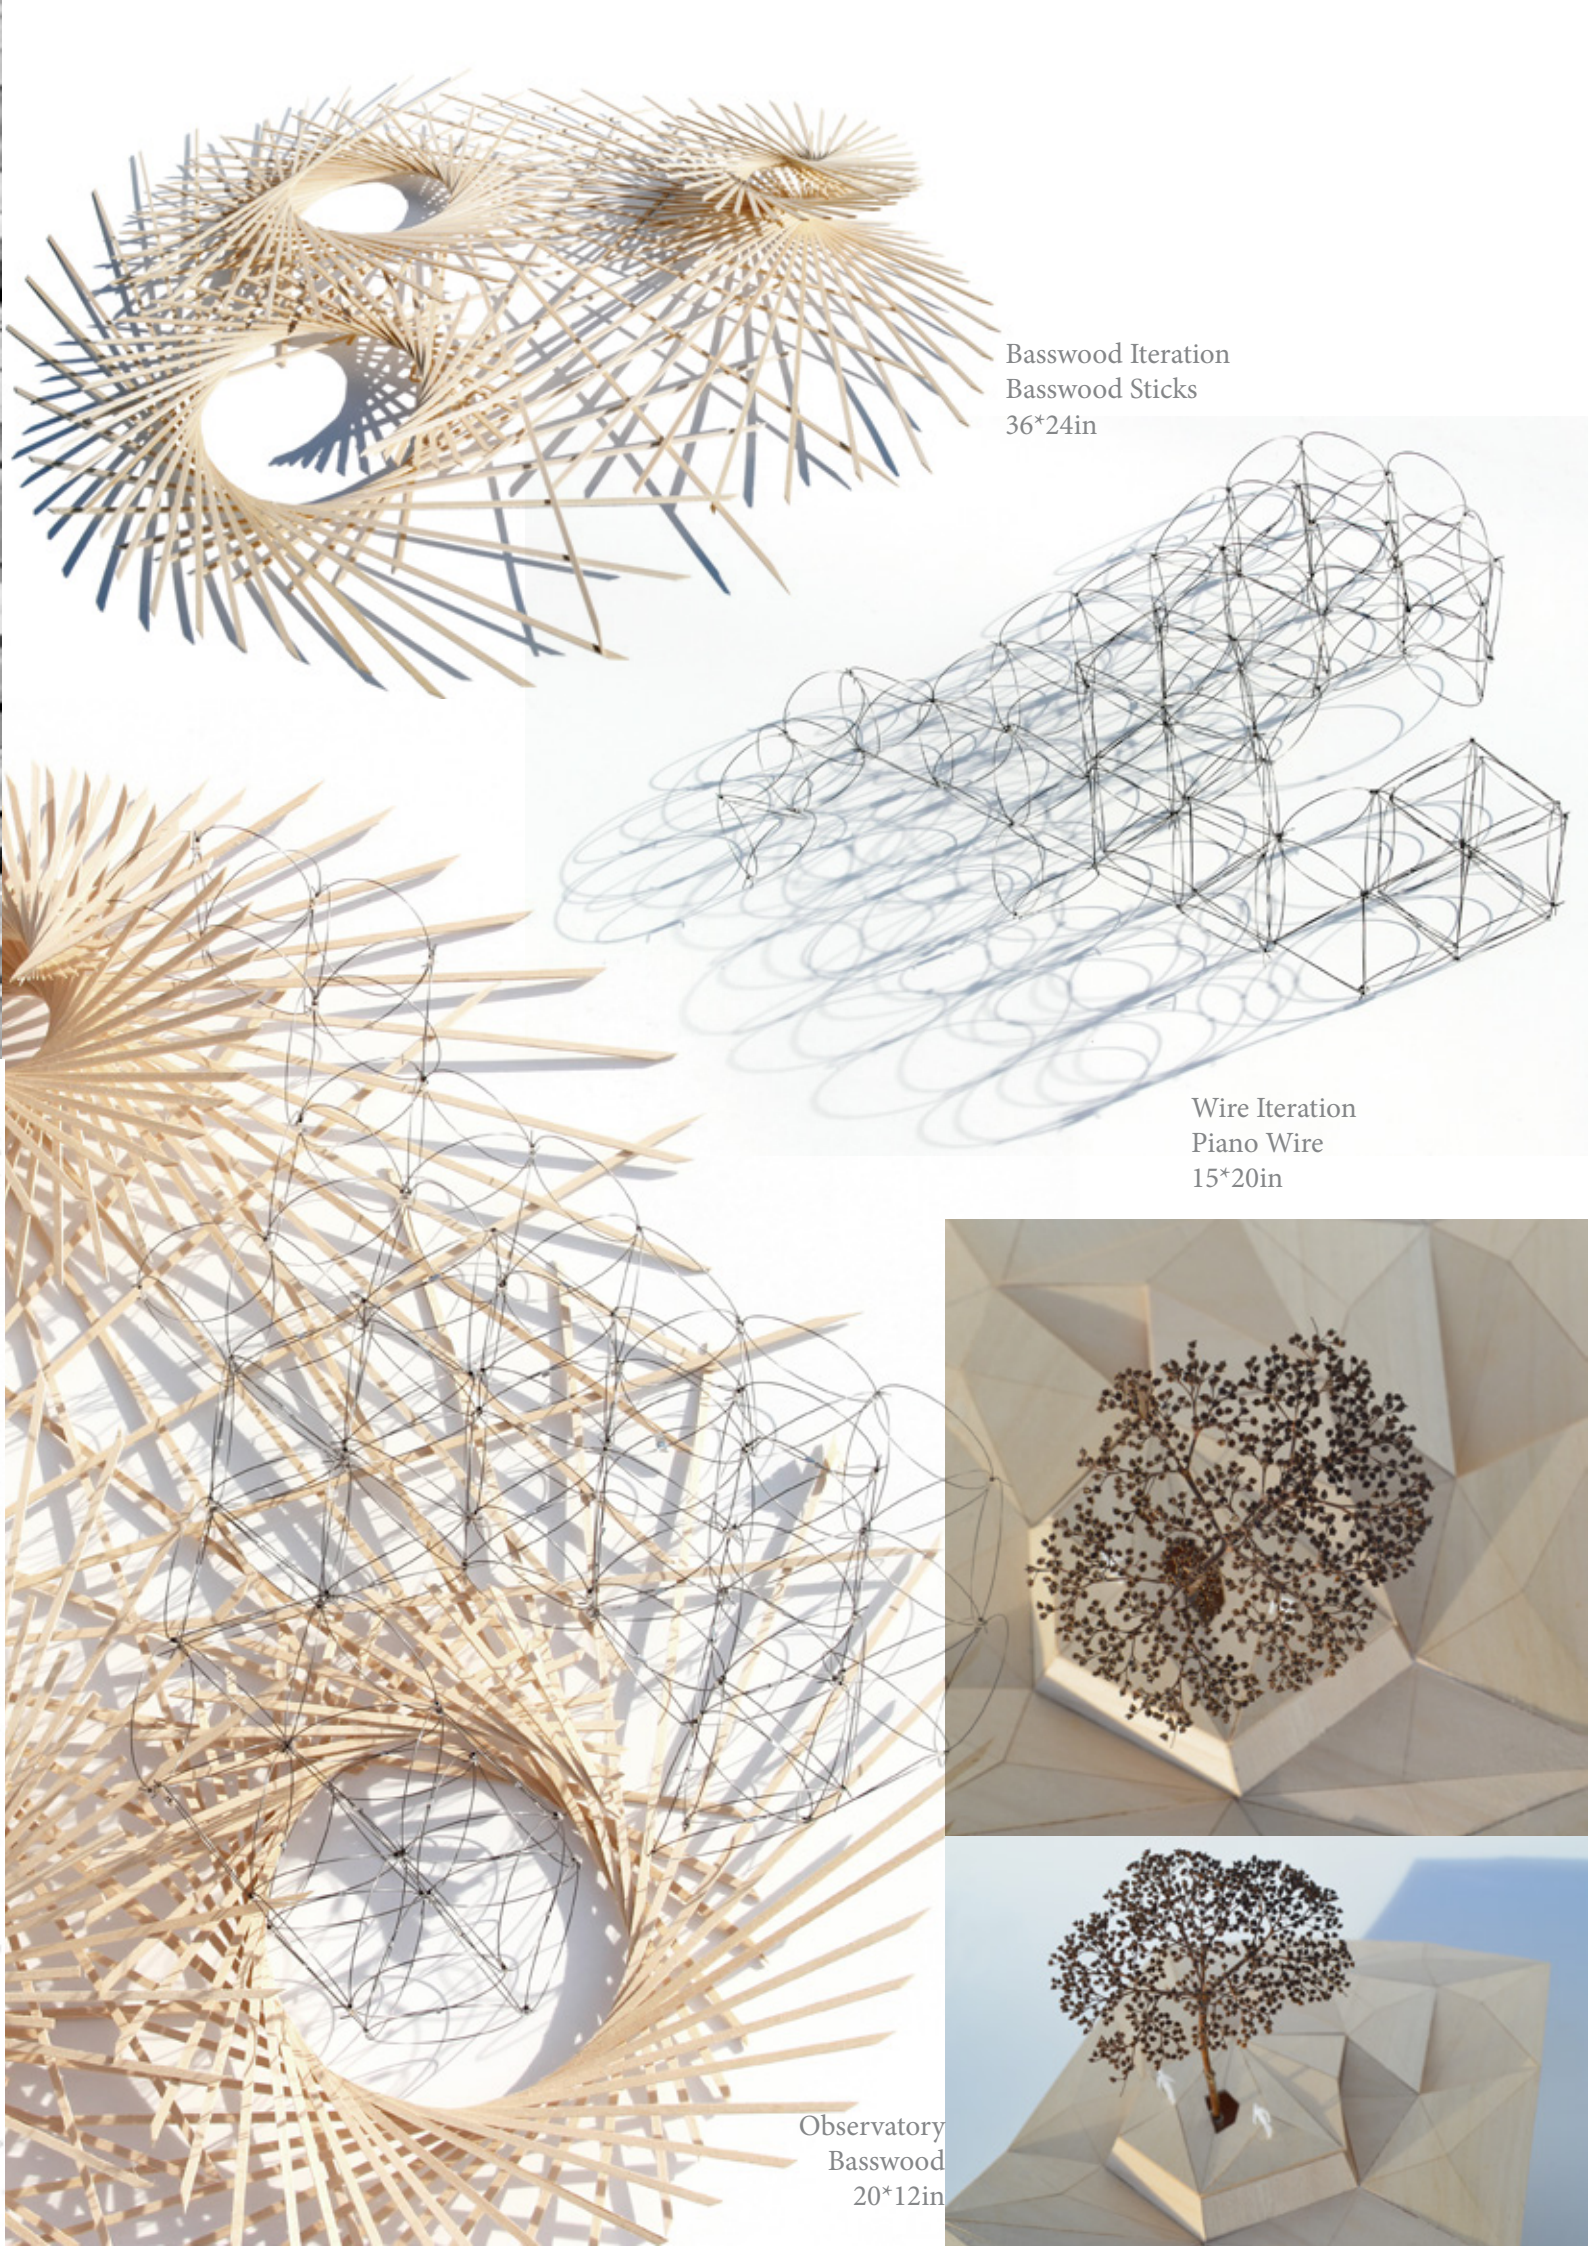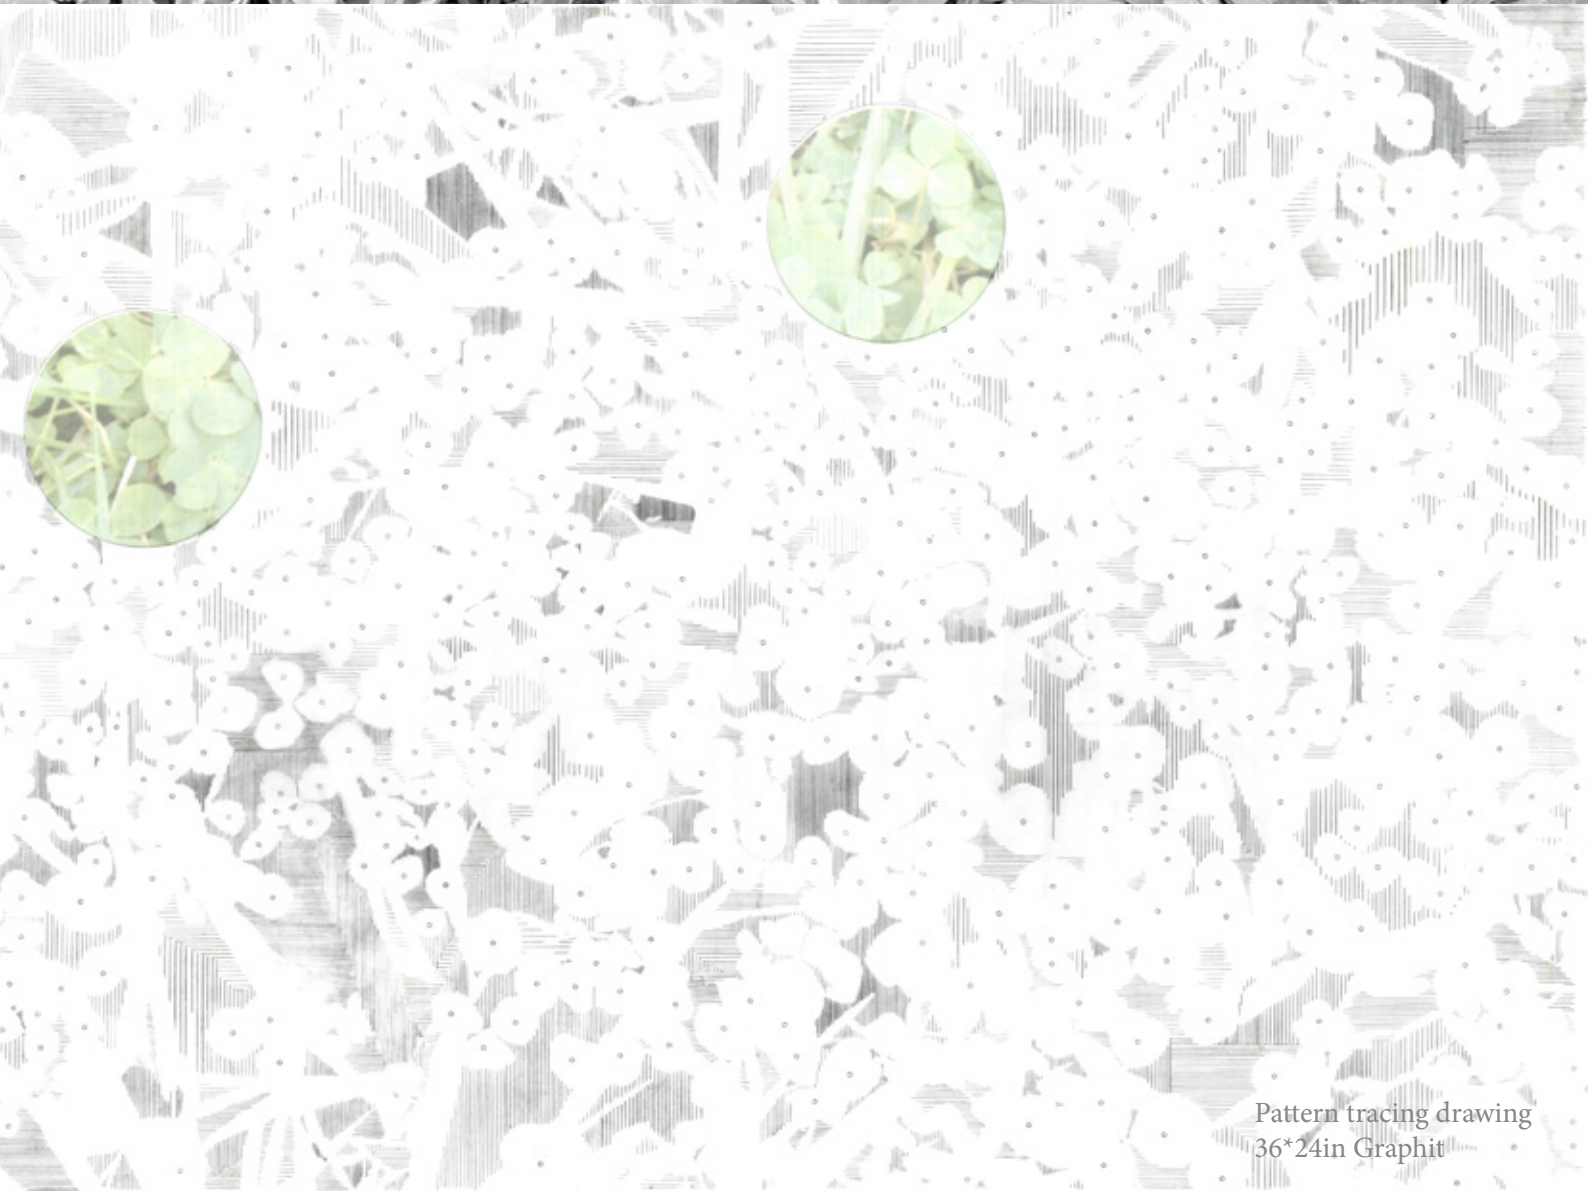

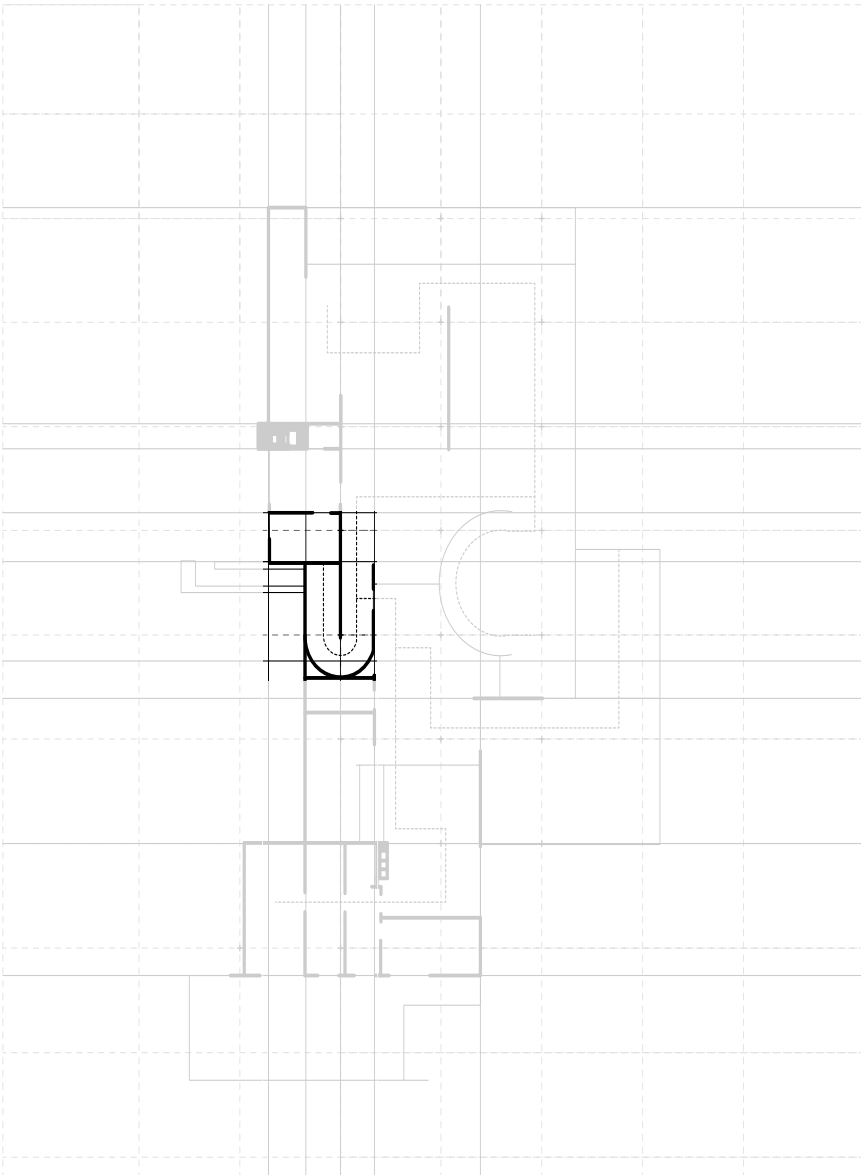

Tugendhat House
Mies Van der Rohe
Brno, Czech Republic



Theater with Two Characters

Studio 211 | 2017 Fall
Nathaniel Elberfeld


The project of theater is inspired by the “scars” on the walls, creating a space by pushing into the porche which is provided as the primary circulation.

Starting from a study prototype from Mies Van der Rohe, the study model derives from the original plan to two separate parts, and these parts progress to a more reasonable model.

The light study is able to grant the theater two characters: one with shadow and the other one with light.

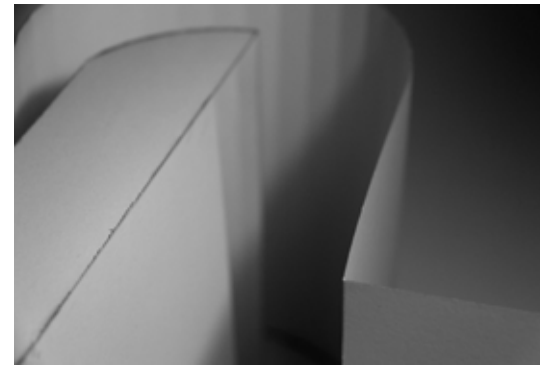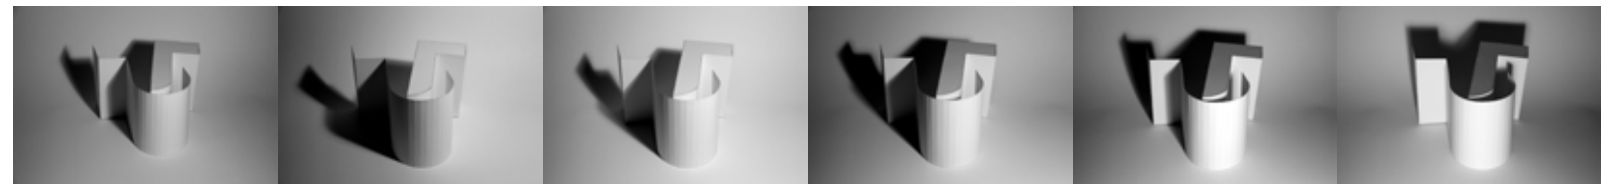


1/16”=1’-0” scale model, White Bristol
Initial shadow study provides a good reference for the visible “scars” portained by light. Two characters, light and shadow, intertwine with each other to create a distinctive boundary.

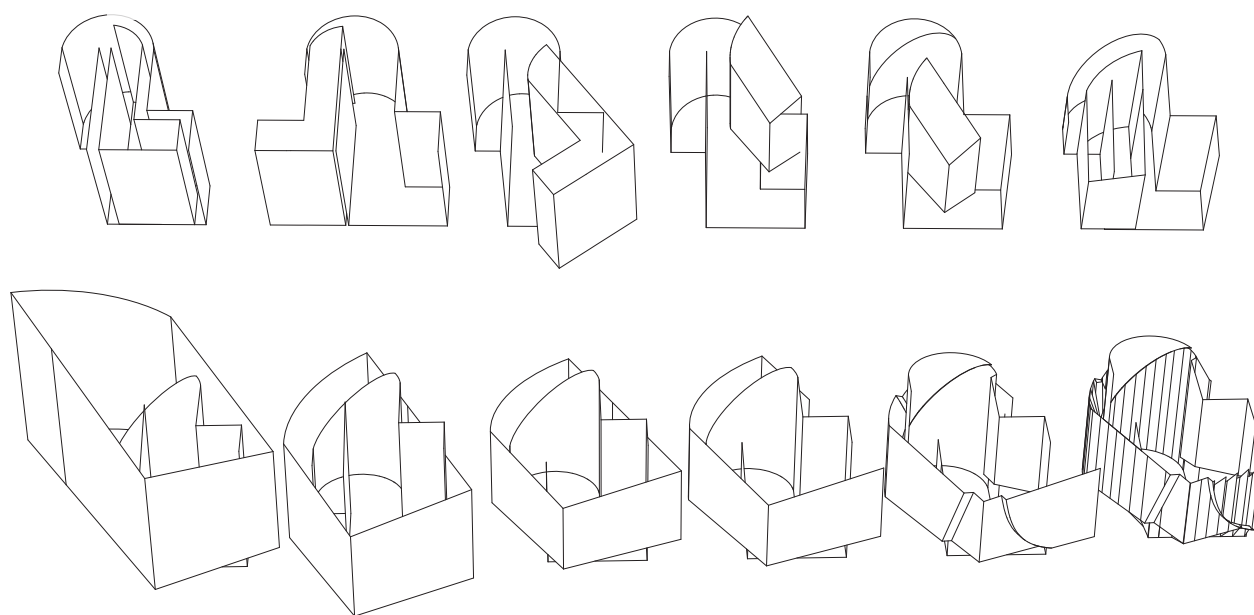

Form Transformation



Barcelona Pavilion,
Barcelona, Spain.




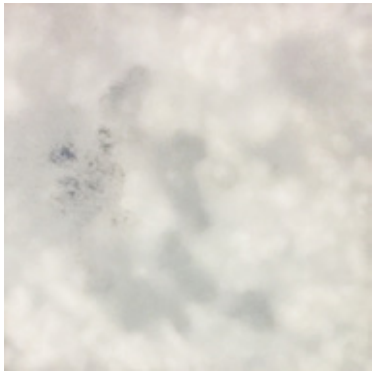


Derived Pattern Scan
I




Derived Pattern Scan
II


The theater is designed according to the arrangement of the sidewalk and goes along with its orientation. The circulations all happen in the porche in between the outer shell and the inner space. This hierarchy distinguishes private and public also provides natural sun-light during the day for the theater. At night, people could see the light in the theater from the street. The two light conditions characterizes this amphitheater.

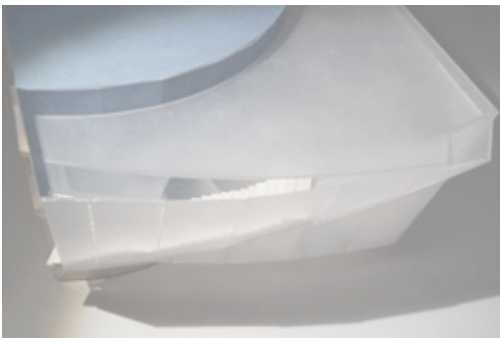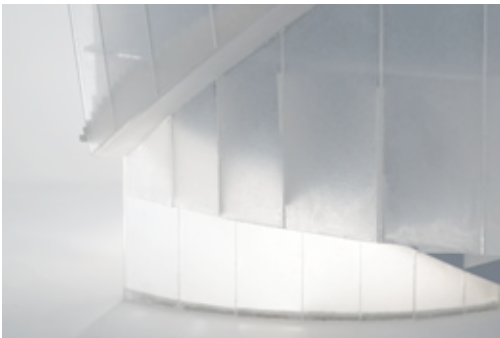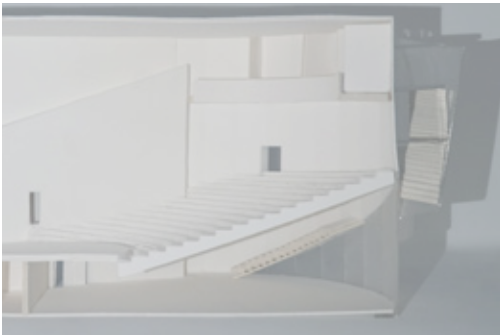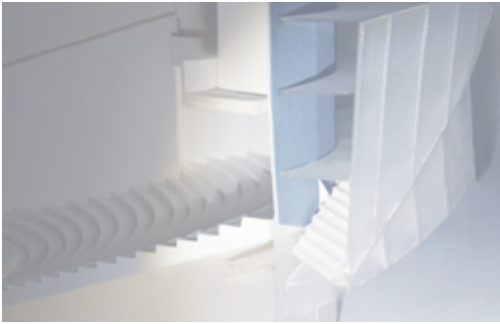


Theater Section Model Photos
1/8" = 1'-0" Scale

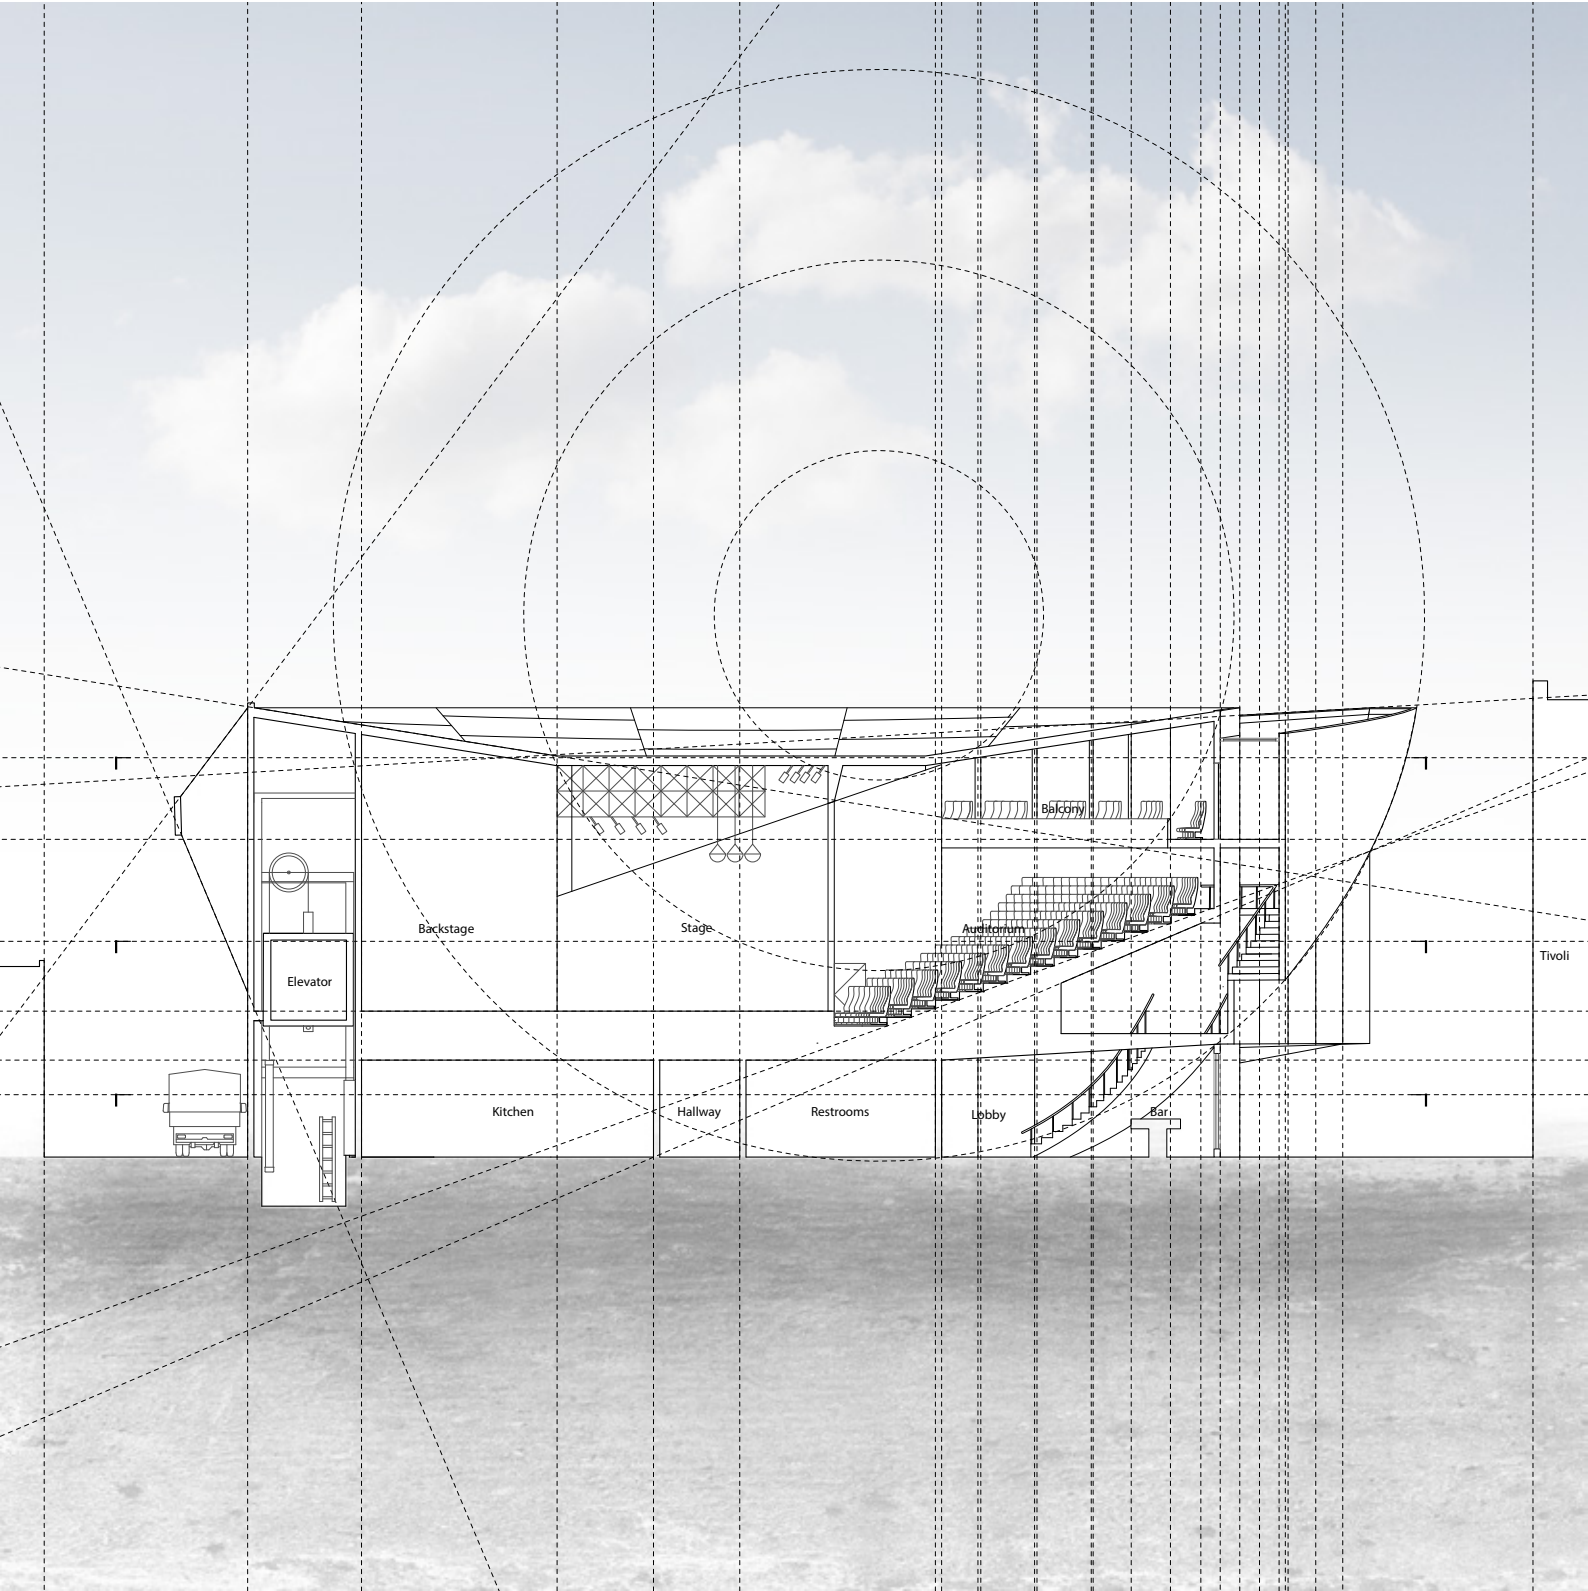


Section Drawing

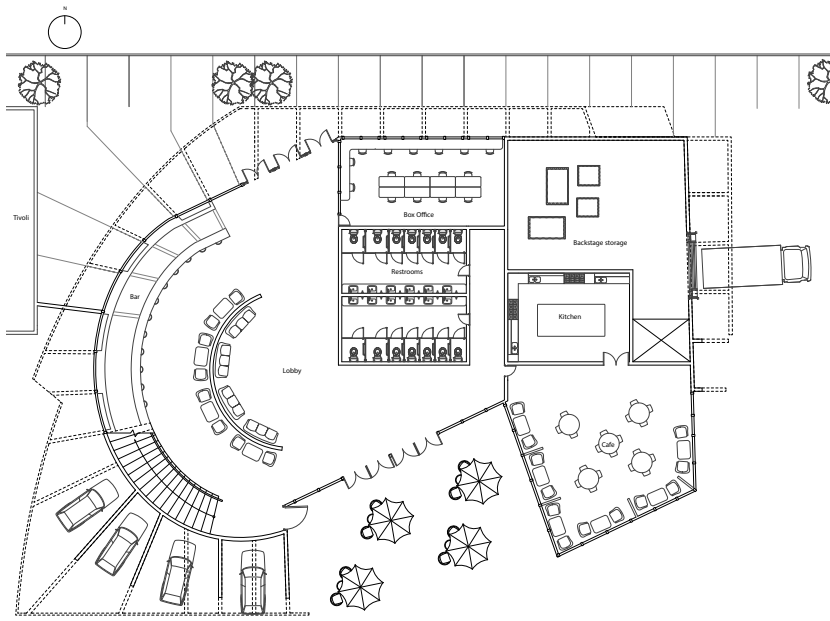

Ground Floor

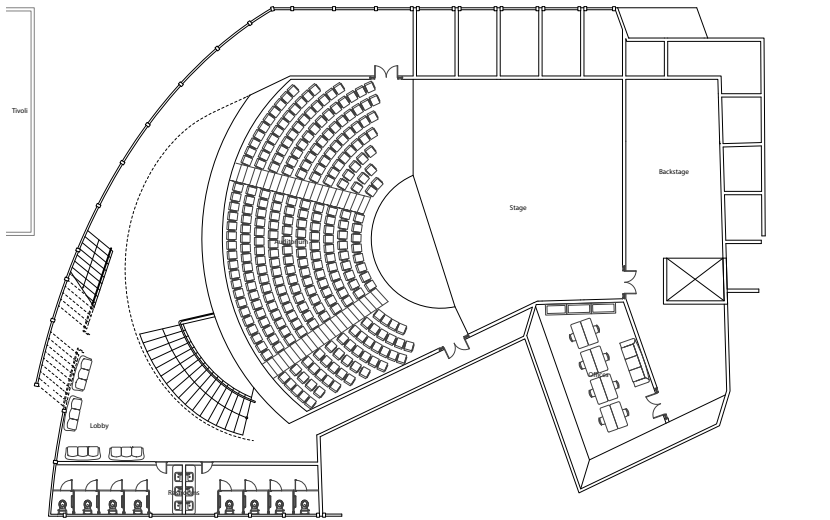

Second Floor

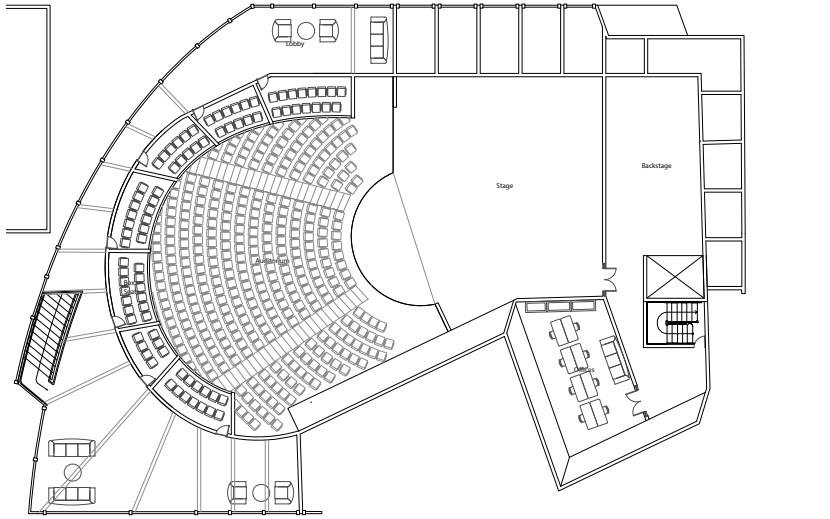

Third Floor

Floor Plans


4101 Laclede
Building Systems | 2018 Fall
Ross Welch
Partners: Zinan Chi
Wentao Guo

Located at one of the busiest area in St. Louis, this modern, luxury residence are surrounded by restaurants, bars, pharmacies and post office. In addition to convinient transportation, the Central West End neighborhood is right next to Cortex, BJC Hospital, Euclid Shopping Corridor, Forest Park, Washington University Medical School, SLU, and many other Public Services.



Surroundings




Wind Study

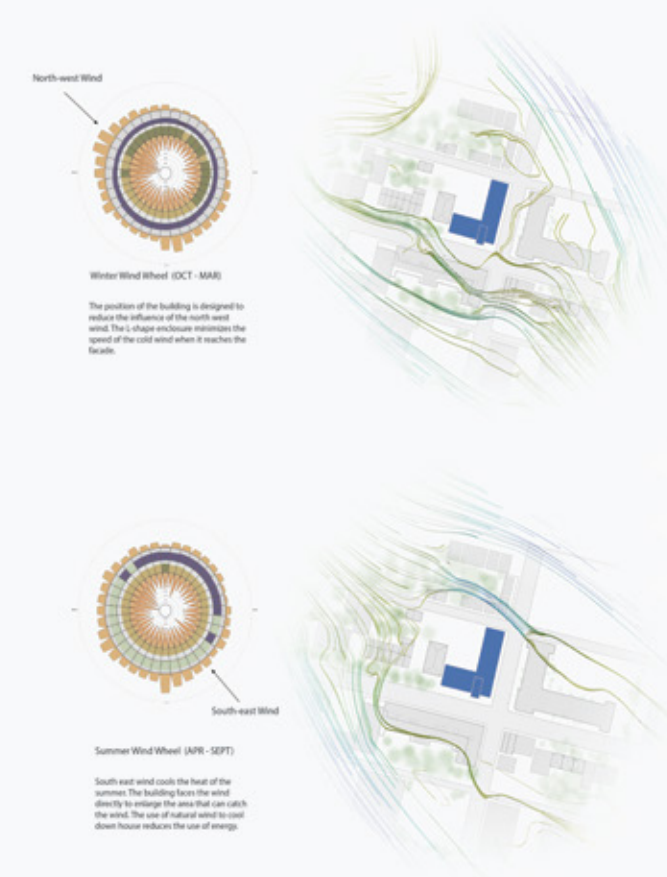

Shadow Study

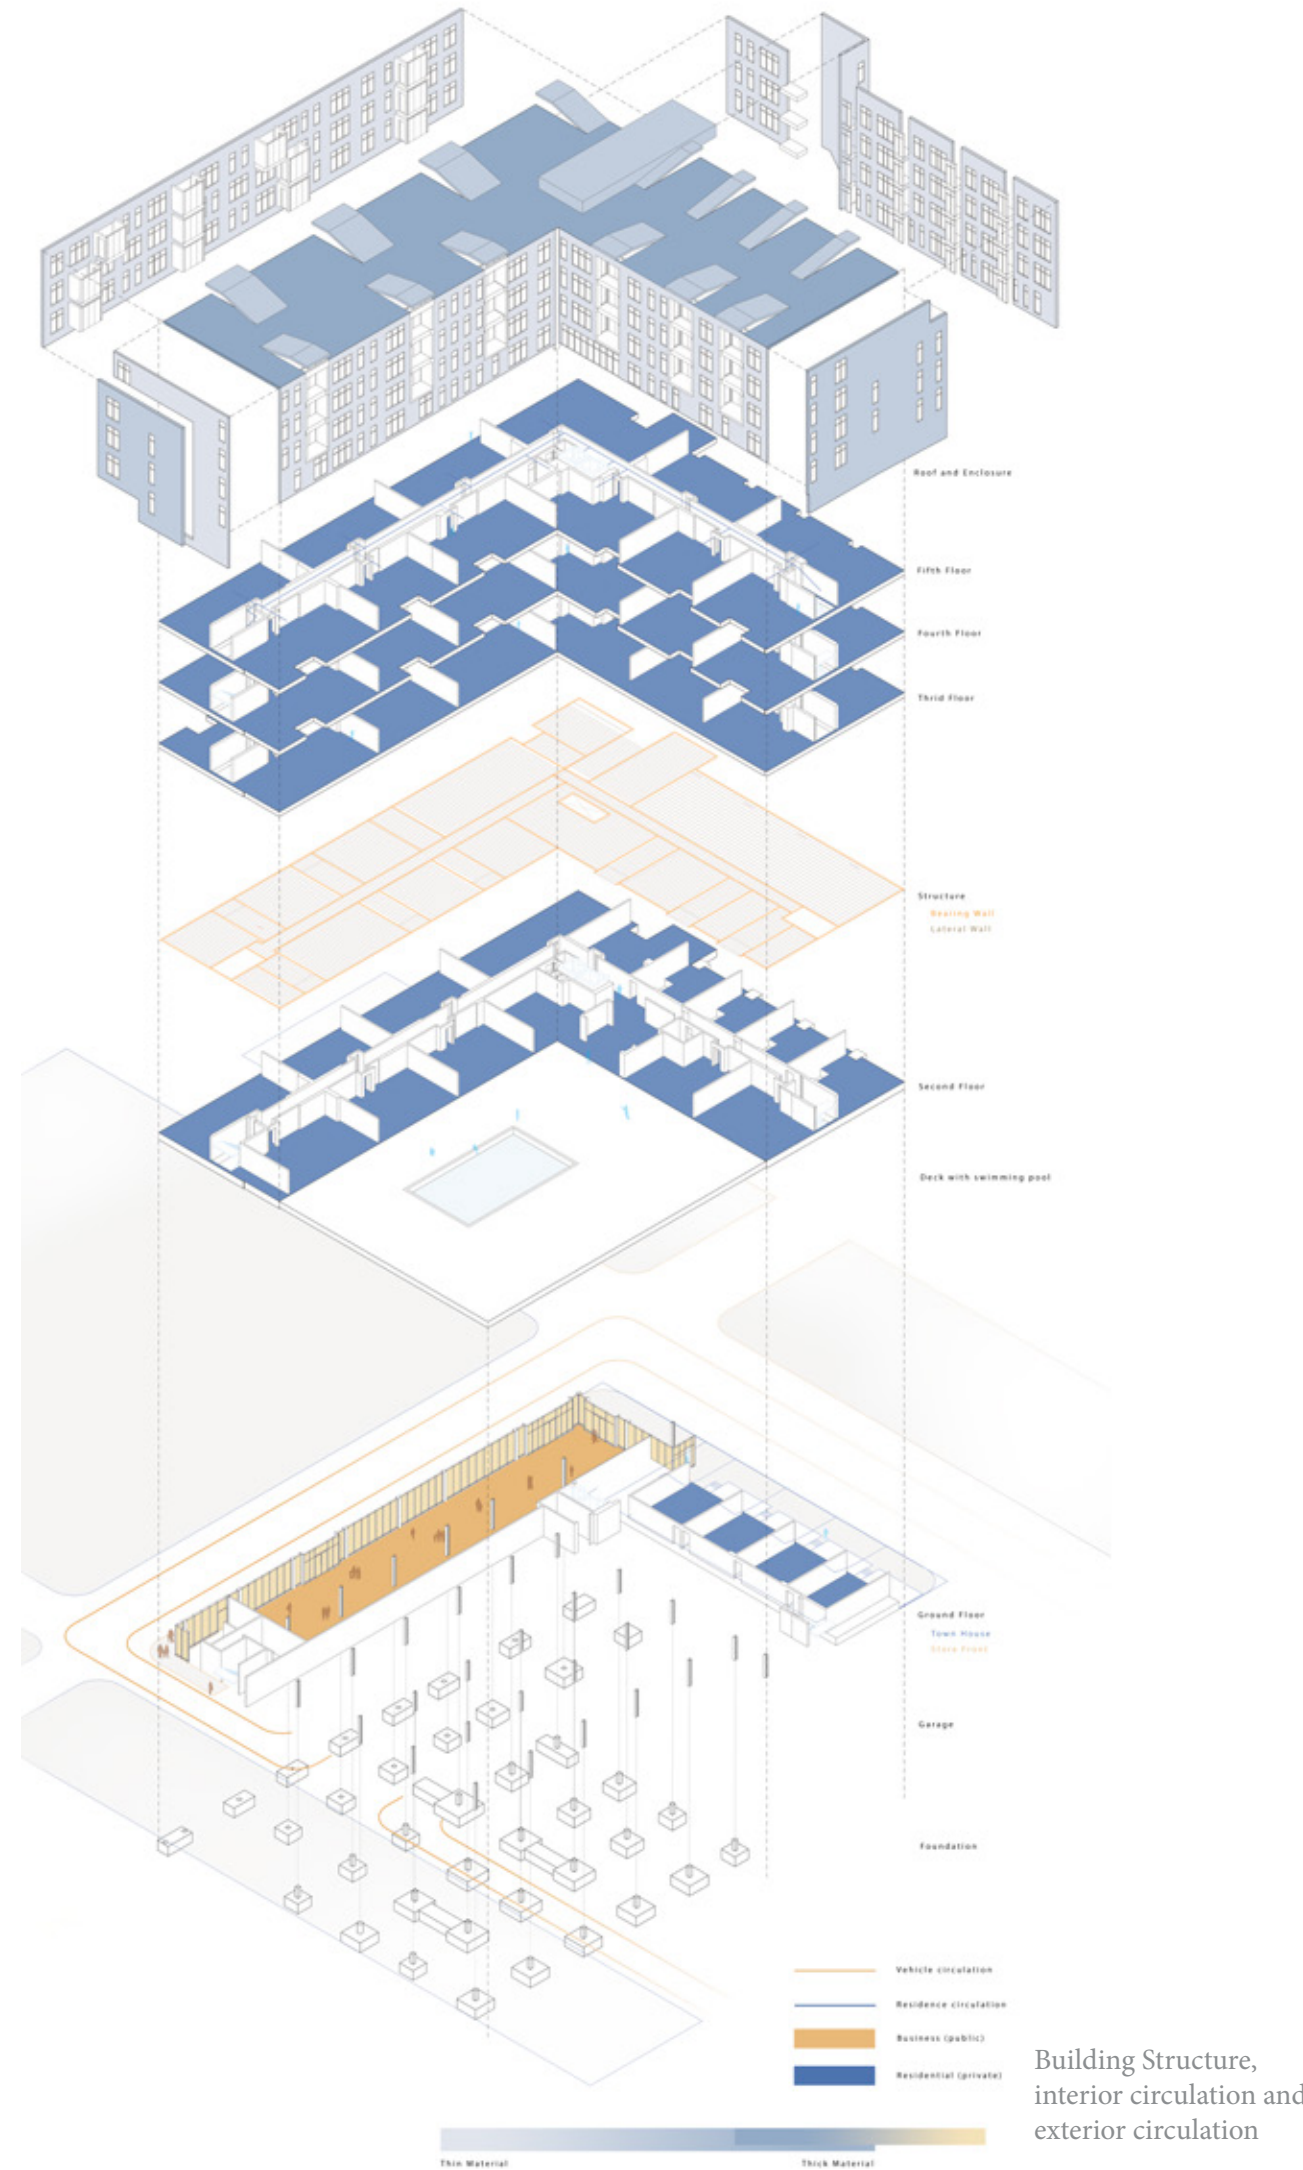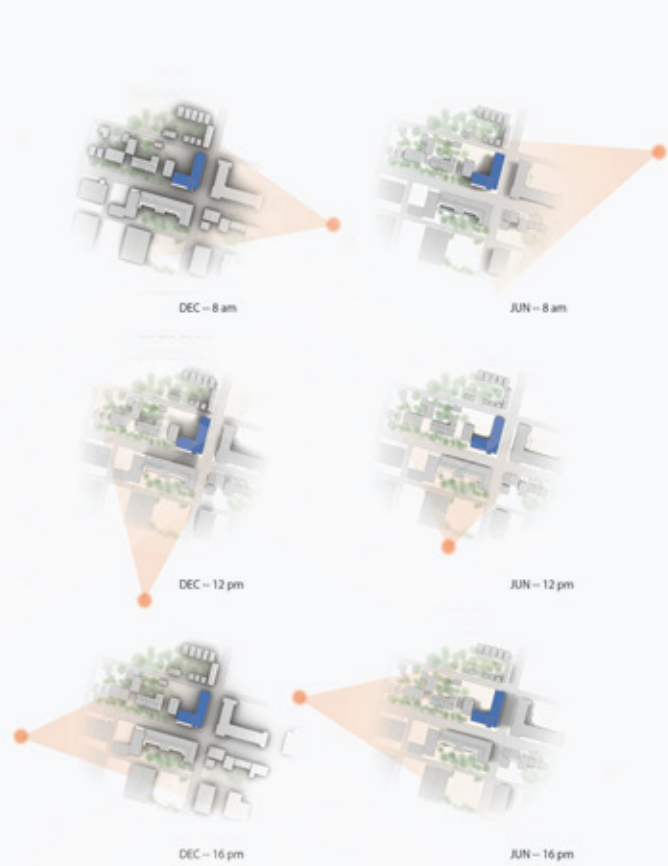


Building Structure, interior circulation and exterior circulation

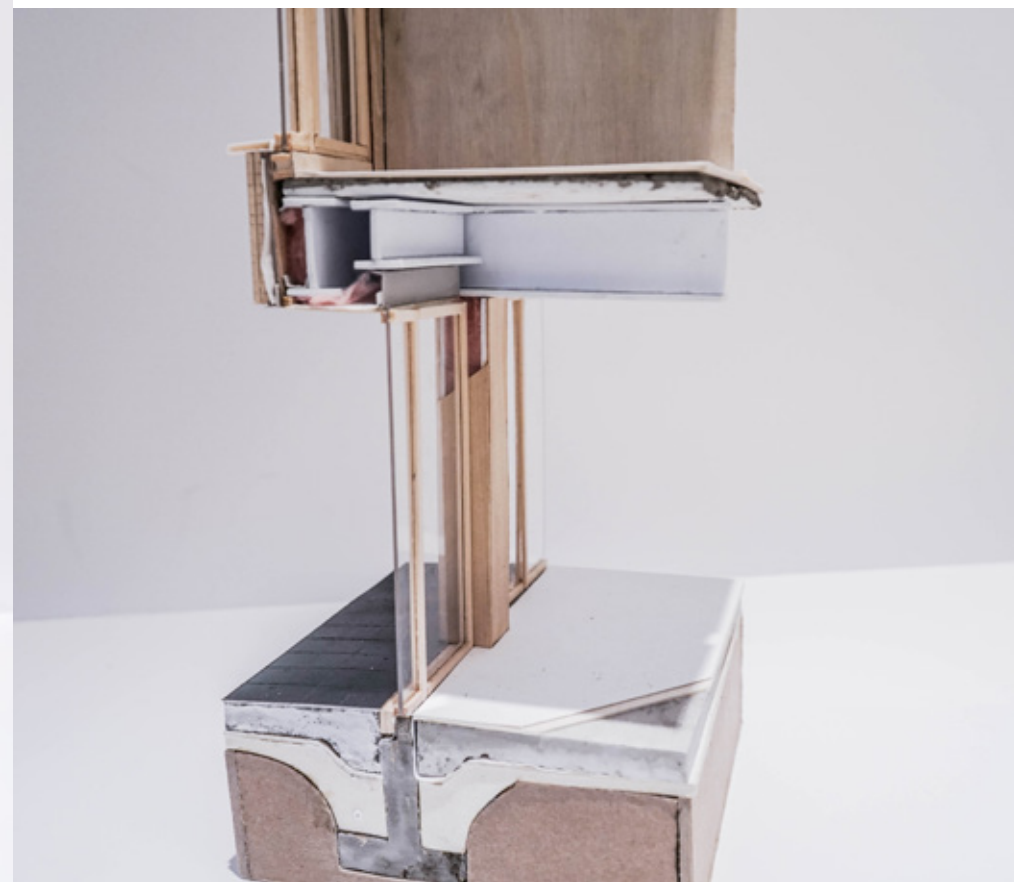

Model details

Wall section scale model
3/2"=1'-0"

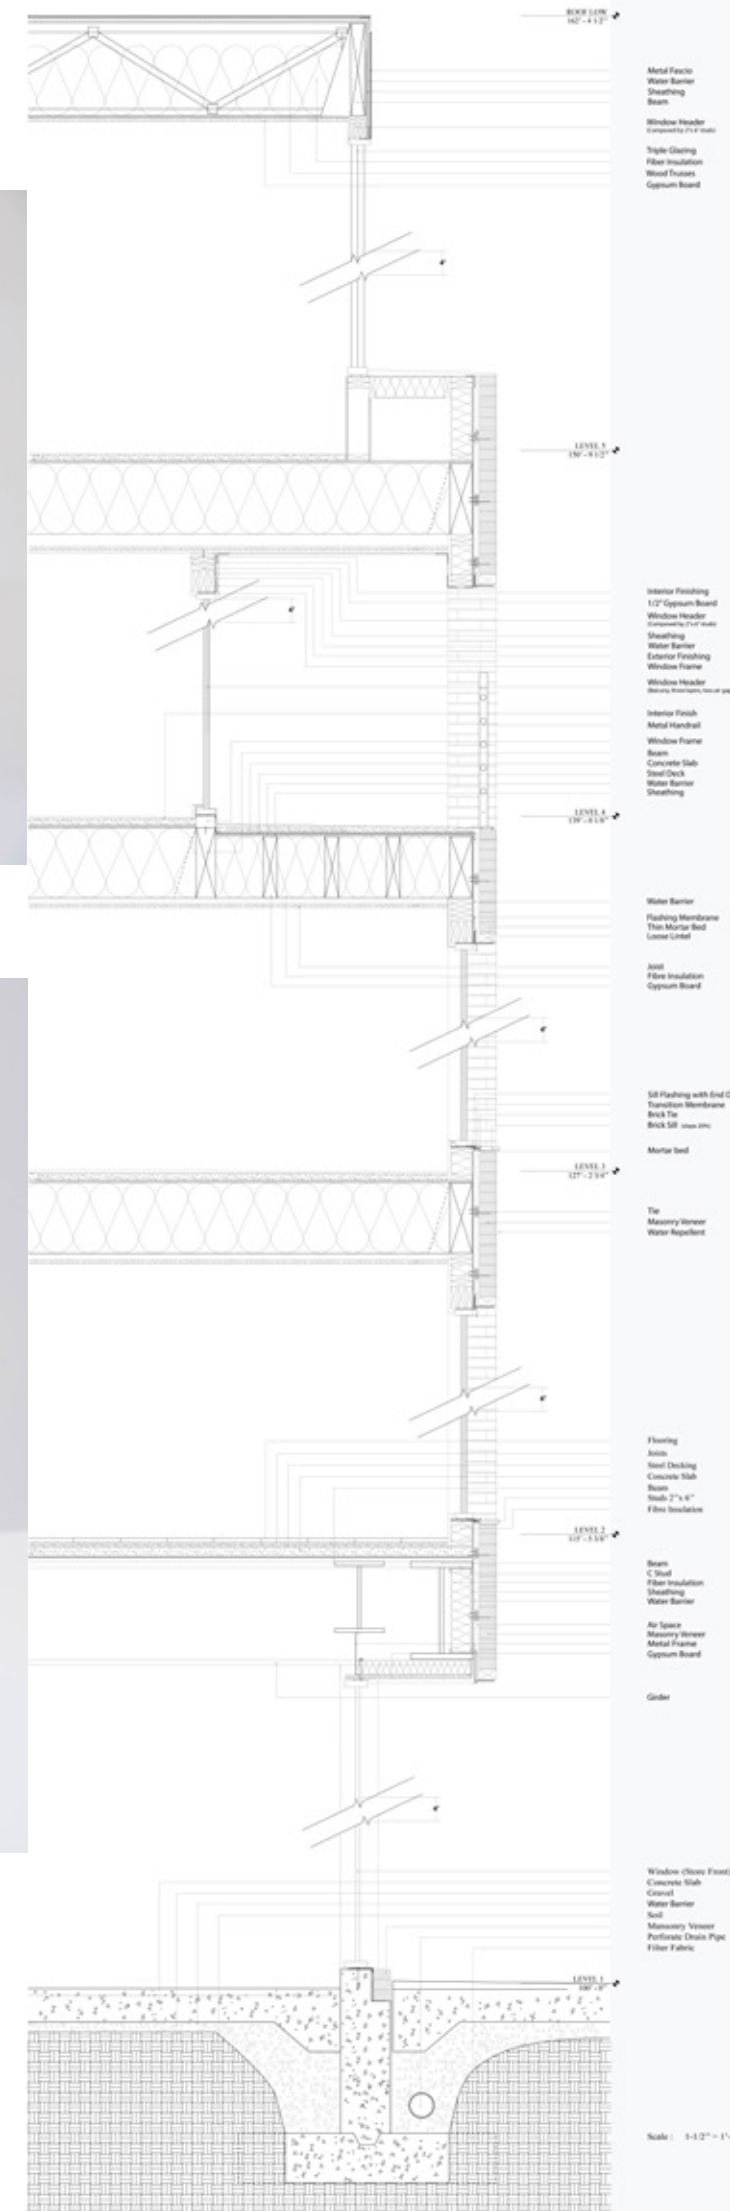

Section Study


4101 Laclede is built in a combination of wood frame and steel frame. This choice of structural frame is mainly under consideration of building function. 4101 Laclede is constructed in steel frame for retailers on the first floor taking the advantages of the long span of steel frame. From the second floor to the fifth, the residential part is constructed in wood frame.



Plywood



Stud 2"x6"

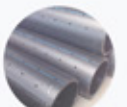

Perforate Drain Pipe



Vapor Retarder



Cyprium



Fiber Insulation



Concrete




Masonry Veneer



Mortar



Triple Glazing

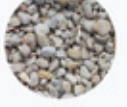

Gravel



Steel Decking

Scale: 3/4"=1'-0"

Wall section drawing

Snail Rocker

Furniture Design | 2017 Fall
Lindsey Stouffer

Starting from the snail shell, the rocker has been modified according to its function and shape. Bend wood technique creates many more possibilities to the realm of furniture design and architecture.



Structural Model



Final Model













-SIRTY PERCENT SUGARY-



-SIRTY PERCENT SUGARY-



-SIRTY PERCENT SUGARY-





-SIRTY PERCEN SUGARY-



-SIRTY PERCEN SUGARY-



-SIRTY PERCEN SUGARY-









